OPRAVA PROPUSTKU KM 36,589
M 1:50

PODÉLNÝ ŘEZ PROPUSTKEM (P13)

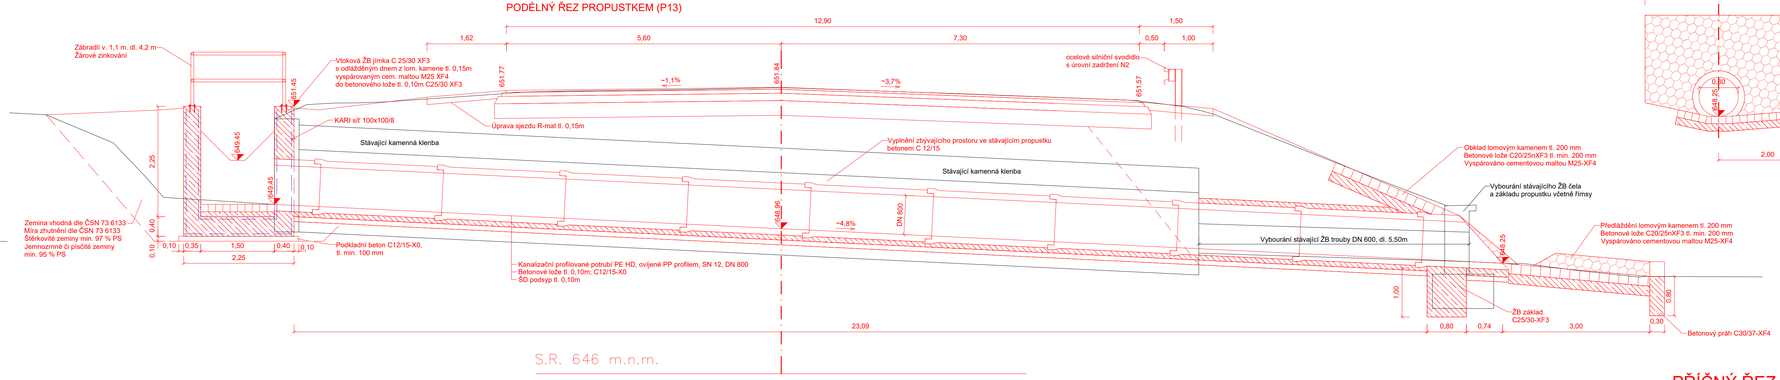

POHLED NA ČELO ODTOKU
M 1:50

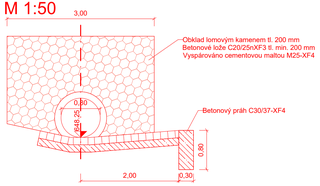

POHLED NA VTOKOVOU JÍMKU
M 1:50

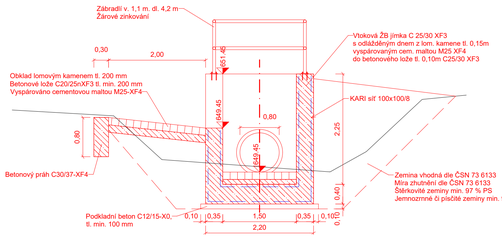

PŘÍČNÝ ŘEZ PROPUSTKEM
M 1:50

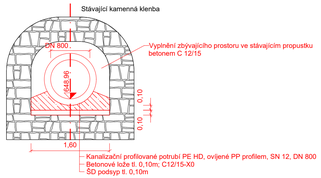

PŘÍČNÝ ŘEZ PROPUSTKEM (P13)

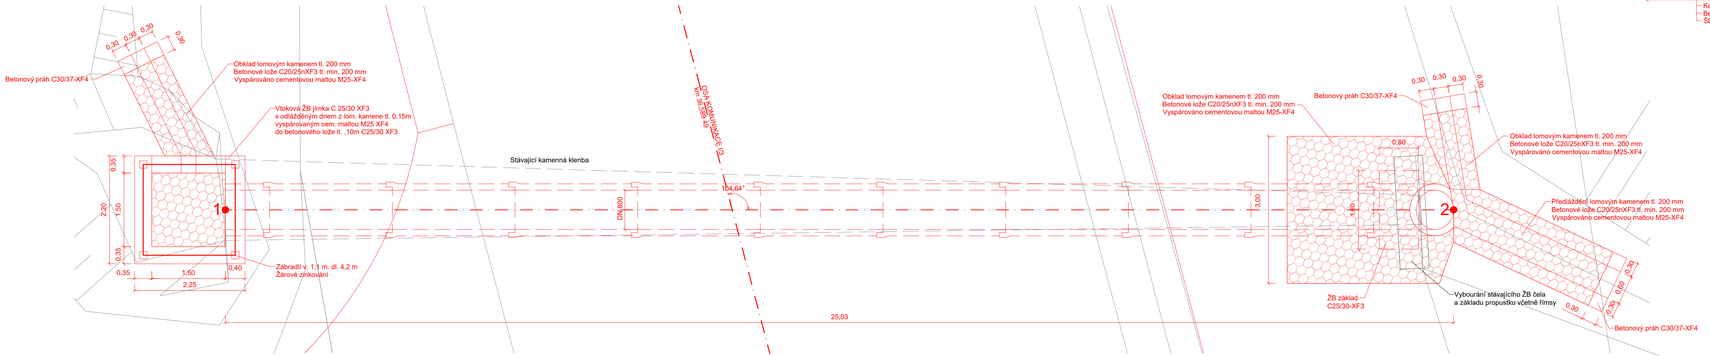

	Y	X	Z
1	-1098340.5576	-733026.7104	469,45
2	-1098349.6336	-733003.3825	648,25

POZNÁMKA:
Jímka propustku je vyztužena KARI sítí 100x100/8 při povrchu.

a			
b			
c			
č.	text změny - odůvodnění	datum	podpis

Název stavby: **I/3 Votice - Oldřichovec oprava povrchu a odvodnění komunikace**

Číslo objektu: **102**

Objednatel stavby:
ŘEDITELSTVÍ SILNIC A DÁLNIC
ŘEDITELSTVÍ SILNIC A DÁLNIC s. p.
Čerčanská 2023/12, 140 00 Praha 4 - Krč
Razítko:
Kontrolovat:
Datum: Podpis:

Zhotovitel stavby:
M - SILNICE
M - SILNICE a.s.
Husova 1697, Bílé Předměstí, 530 03 Pardubice
Razítko:
M - SILNICE a.s.
Husova 1697
IČO 421 96 868
Městský soud v Praze
Třebonická 290/21, 190 15 Praha 9
Kontrolovat:
Datum: Podpis:

Koordinátor RDS:
M - PROJEKCE
M - PROJEKCE s.r.o.
Resslova 956/13, 500 02 Hradec Králové
Razítko:
Kontrolovat:
Datum: Podpis:

KONCEPT

Souřadnicový systém S-JTSK, Výškový systém Bpv

Navrhl/vypracoval: Karel Láska, Podpis:	Zodpovědný projektant: Karel Láska, Podpis:	Generální ředitel: ING. PETR HÁJEK, Ředitel ateliéru Liberec: ING. JIŘÍ EHRENBERGER	Zhotovitel: M - PROJEKCE s.r.o. Resslova 956/13, 500 02 Hradec Králové
Technická kontrola: DAVID SENOHRÁBEK, DiS, Podpis:	Hlavní inženýr projektu: Karel Láska, Podpis:		

Kraj: STŘEDOČESKÝ KRAJ		Čís. zakázky:	26-024-02
Katast. úz.: Votice, Hostišov, Kouty u Smilkova		Čís. akce:	-
Objednatel: M - SILNICE a.s., Husova 1697, Bílé Předměstí, 530 03 Pardubice		Datum:	03/2026
Objekt: **SO 102 Oprava propustků**		Formát:	10x A4
		Měřítko:	1:50
		Stupeň: **RDS**	Souprava:
Příloha: **Propustek v km 36,589**		Čís. přílohy: **2.7**	