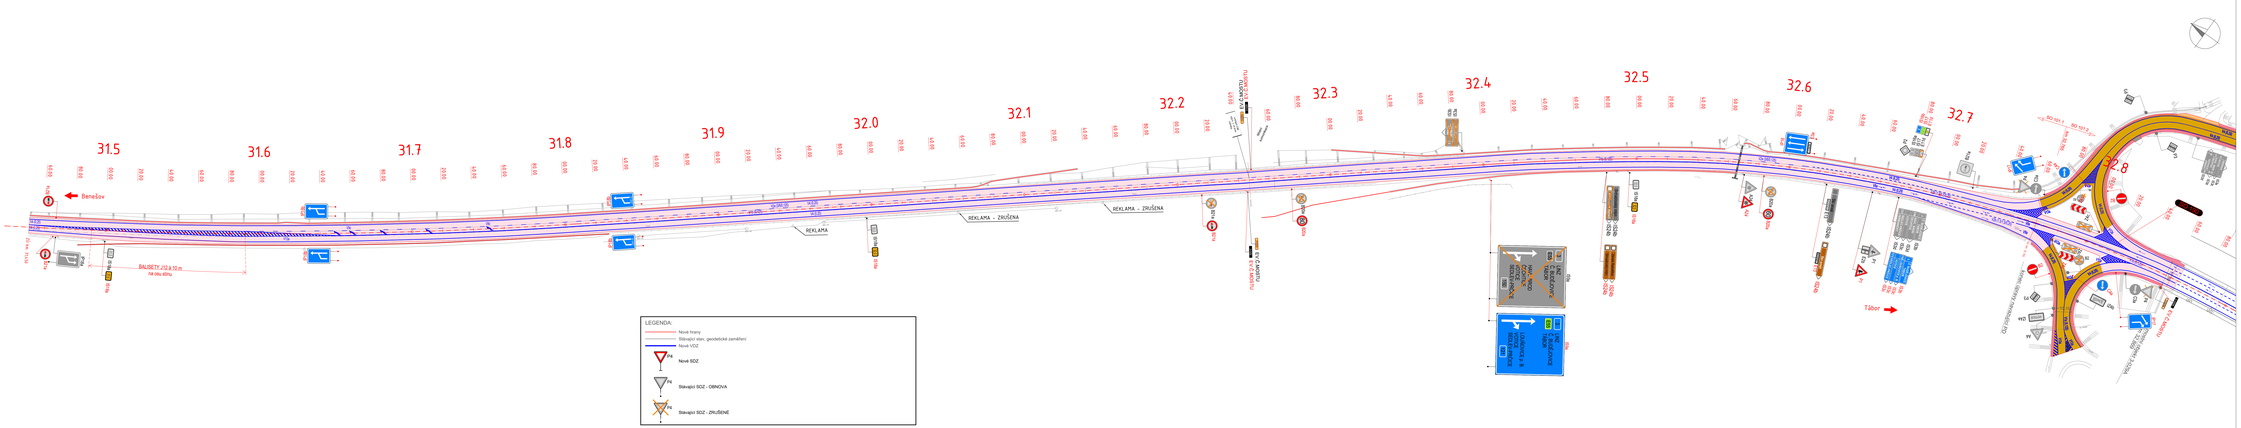

a			
b			
c			
d	text změny - odůvodnění	datum	podpis

Název stavby: **I/3 Votice - Oldřichovec oprava povrchu a odvodnění komunikace**	Číslo objektu: **190**

Objednatel stavby: ŘEDITELSTVÍ SILNIC A DÁLNIC **ŘEDITELSTVÍ SILNIC A DÁLNIC s. p.** Čerčanská 2023/12, 140 00 Praha 4 - Kč	Razítko: Kontroloval: Datum: Podpis:
Zhotovitel stavby: M - SILNICE **M - SILNICE a.s.** Husova 1697, Bílé Předměstí, 530 03 Pardubice	Razítko: M - SILNICE a.s. Pardubice, Husova 1697 IČO: 27364311 Tel/Fax/Email: 466 00 [illegible] Trmalovská 2562/21, 190 12 Praha 9 Kontroloval: Datum: Podpis:
Koordinátor RDS: M - PROJEKCE **M - PROJEKCE s.r.o.** Resslova 958/13, 500 02 Hradec Králové	Razítko: Kontroloval: Datum: Podpis:

KONCEPT

Součástí projektové dokumentace je soubor Excel s názvem „Soupis prací - Výkaz výměr.xlsx"

Hlavní inženýr projektu: Karel Laška Podpis:	Odpovědný projektant: Karel Laška Podpis:	Generální ředitel: Ing. PETR HÁJEK Ředitel závodu Liberec: Ing. JIŘÍ EHRENBERGER	Zhotovitel: M - PROJEKCE M - PROJEKCE s.r.o. Resslova 958/13, 500 02 Hradec Králové
Technická kontrola: DAVID SENOHRABEK, DiS Podpis:	Hlavní inženýr projektu: Karel Laška Podpis:		

Kraj: STŘEDOČESKÝ KRAJ		Čís. zakázky:	26-024-02
Katast. úz.: Votice, Hostišov, Kouty u Smilkova		Čís. akce:	
Objednatel: M - SILNICE a.s., Husova 1697, Bílé Předměstí, 530 03 Pardubice		Datum:	03/2026
Objekt: **SO 190 Svislé s vodorovné dopravní značení v km 31,450 - 37,357**		Formát:	8x A4
		Měřítko:	1:1000
		Stupeň: **RDS**	Dopravce:
Příloha: **Situace dopravního značení Č.1**		Čís. přílohy: **2.1**	