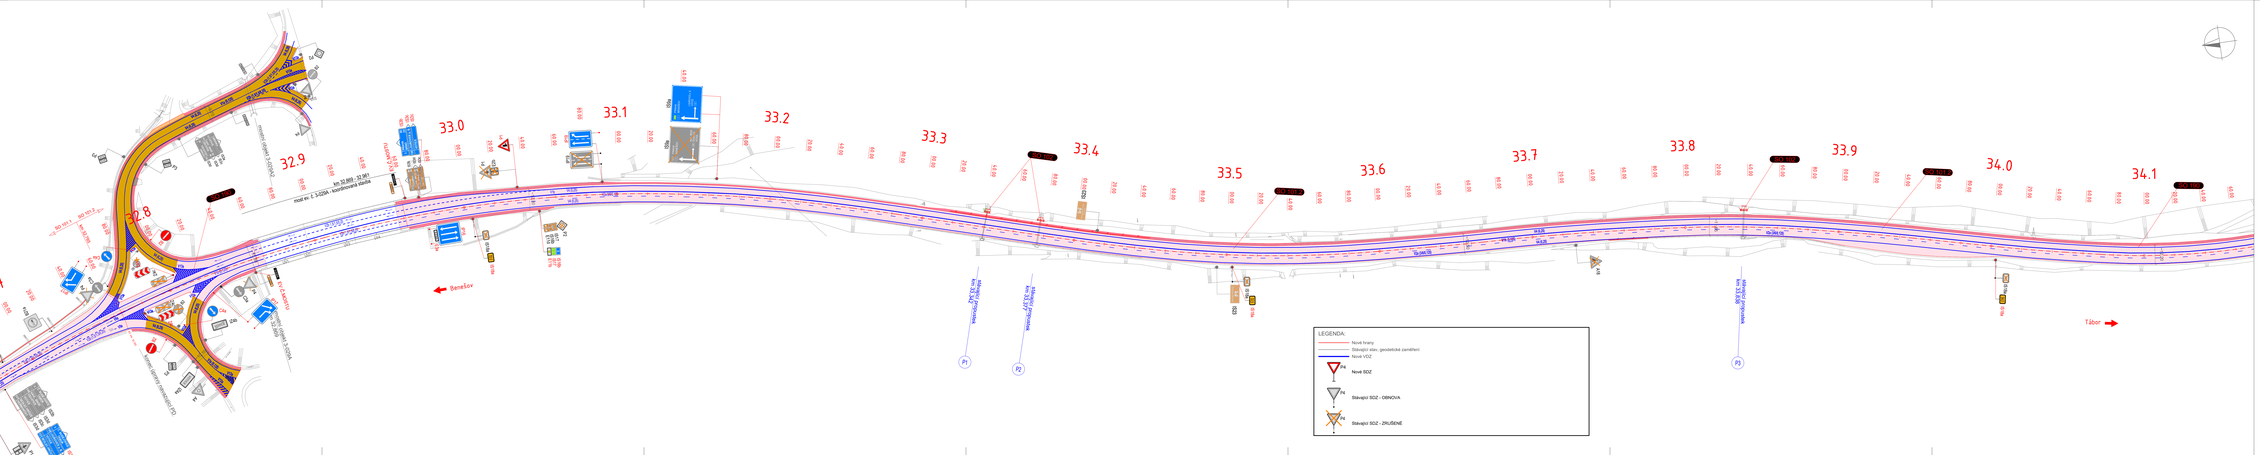

a			
b			
c			
d	text změny - odůvodnění	datum	podpis

Název stavby: **I/3 Votice - Oldřichovec oprava povrchu a odvodnění komunikace**

Číslo objektu: **190**

Objednatel stavby:
ŘEDITELSTVÍ SILNIC A DÁLNIC
ŘEDITELSTVÍ SILNIC A DÁLNIC s. p.
Čerčanská 2023/12, 140 00 Praha 4 - Kč

Zhotovitel stavby:
M - SILNICE a.s.
Husova 1697, Bílé Předměstí, 530 03 Pardubice
M - SILNICE a.s.
Pardubice, Husova 1697
Bílé Předměstí, 530 03
Telefon:(+420) 466 206 111
Trhové Hradec 2562/21, 190 10 Praha 9

Koordinátor RDS:
M - PROJEKCE
M - PROJEKCE s.r.o.
Resslova 958/13, 500 02 Hradec Králové

Zodpovědný projektant: Karel Laška
Hlavní inženýr projektu: Karel Laška
Generální ředitel: ING. PETR HÁJEK
Ředitel závodu Liberec: ING. JIŘÍ EHRENBERGER
Zhotovitel: M - PROJEKCE s.r.o. Resslova 958/13, 500 02 Hradec Králové

KONCEPT

Souřadnicový systém S-JTSK, Výškový systém Bpv

Vypracovatel: Karel Laška
Technická kontrola: DAVID SENOHRABEK, DiS

Kraj: STŘEDOČESKÝ KRAJ
Katast. úz.: Votice, Hostišov, Koutu u Smilkova
Objednatel: M - SILNICE a.s., Husova 1697, Bílé Předměstí, 530 03 Pardubice
Objekt: **SO 190 Svislé s vodorovné dopravní značení v km 31,450 - 37,357**
Příloha: **Situace dopravního značení Č.2**

Čís. zakázky:	26-024-02
Čís. akce:	
Datum:	03/2026
Formát:	8x A4
Měřítko:	1:1000
Stupeň:	RDS
Dopravce:	
Čís. přílohy:	2.2