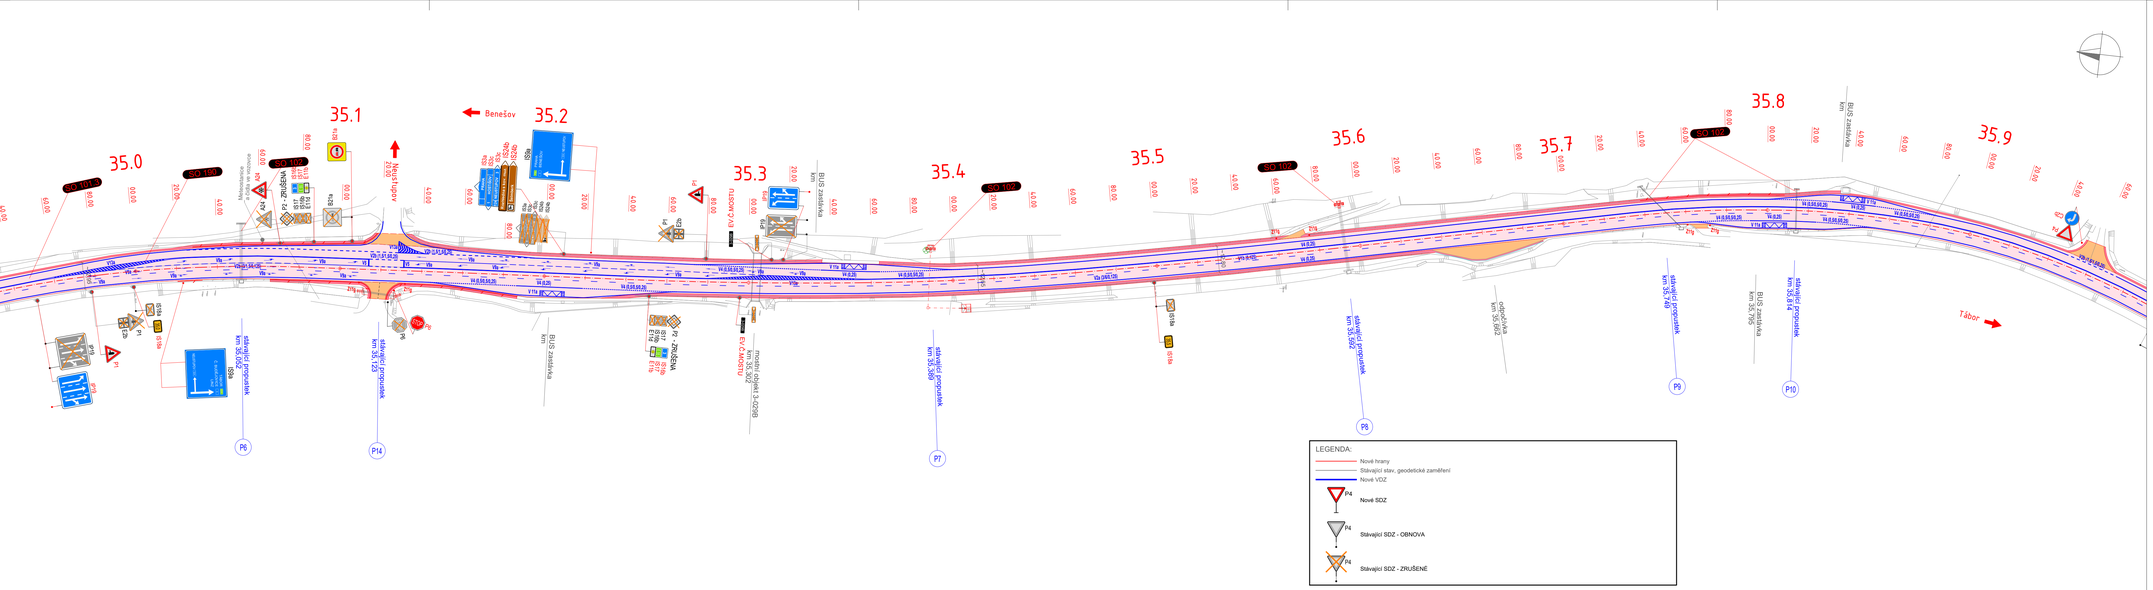

a			
b			
c			
č.	text změny - odůvodnění	datum	podpis

Název stavby: **I/3 Votice - Oldřichovec oprava povrchu a odvodnění komunikace**

Číslo objektu: **190**

Objednatel stavby:
ŘEDITELSTVÍ SILNIC A DÁLNIC
ŘEDITELSTVÍ SILNIC A DÁLNIC s. p.
Čerčanská 2023/12, 140 00 Praha 4 - Krč

Razítko:
Kontrolovat:
Datum: Podpis:

Zhotovitel stavby:
M-SILNICE
M - SILNICE a.s.
Husova 1697, Bílé Předměstí, 530 03 Pardubice

Razítko:
M - SILNICE a.s.
Husova 1697, Bílé Předměstí, 530 03 Pardubice
IČO 421 96 868
Mimosoudní subjekt zápisu u Městského soudu v Praze
Třída Kosmonautů 1947, 779 00 Olomouc
Trébenická 2900/1, 190 15 Praha 9
Kontrolovat:
Datum: Podpis:

Koordinátor RDS:
M - PROJEKCE
M - PROJEKCE s.r.o.
Resslova 956/13, 500 02 Hradec Králové

Razítko:
Kontrolovat:
Datum: Podpis:

KONCEPT

Souřadnicový systém S-JTSK, Výškový systém Bpv

Navrhl/vypracoval: Karel Láska	Zodpovědný projektant: Karel Láska	Generální ředitel: ING. PETR HÁJEK	Zhotovitel: M - PROJEKCE s.r.o. Resslova 956/13, 500 02 Hradec Králové
Podpis:	Podpis:	Ředitel ateliéru Liberec: ING. JIŘÍ EHRENBERGER	
Technická kontrola: DAVID SENOHRÁBEK, DIS	Hlavní inženýr projektu: Karel Láska		
Podpis:	Podpis:		

Kraj: STŘEDOČESKÝ KRAJ		Čís. zakázky:	26-024-02
Katast. úz.: Votice, Hostišov, Kouty u Smilkova		Čís. akce:	
Objednatel: M - SILNICE a.s., Husova 1697, Bílé Předměstí, 530 03 Pardubice		Datum:	03/2026
Objekt: **SO 190 Svislé s vodorovné dopravní značení v km 31,450 - 37,357**		Formát:	6x A4
		Měřítko:	1:1000
		Stupeň: **RDS**	Souprava:
Příloha: **Situace dopravního značení Č.4**		Čís. přílohy: **2.4**	