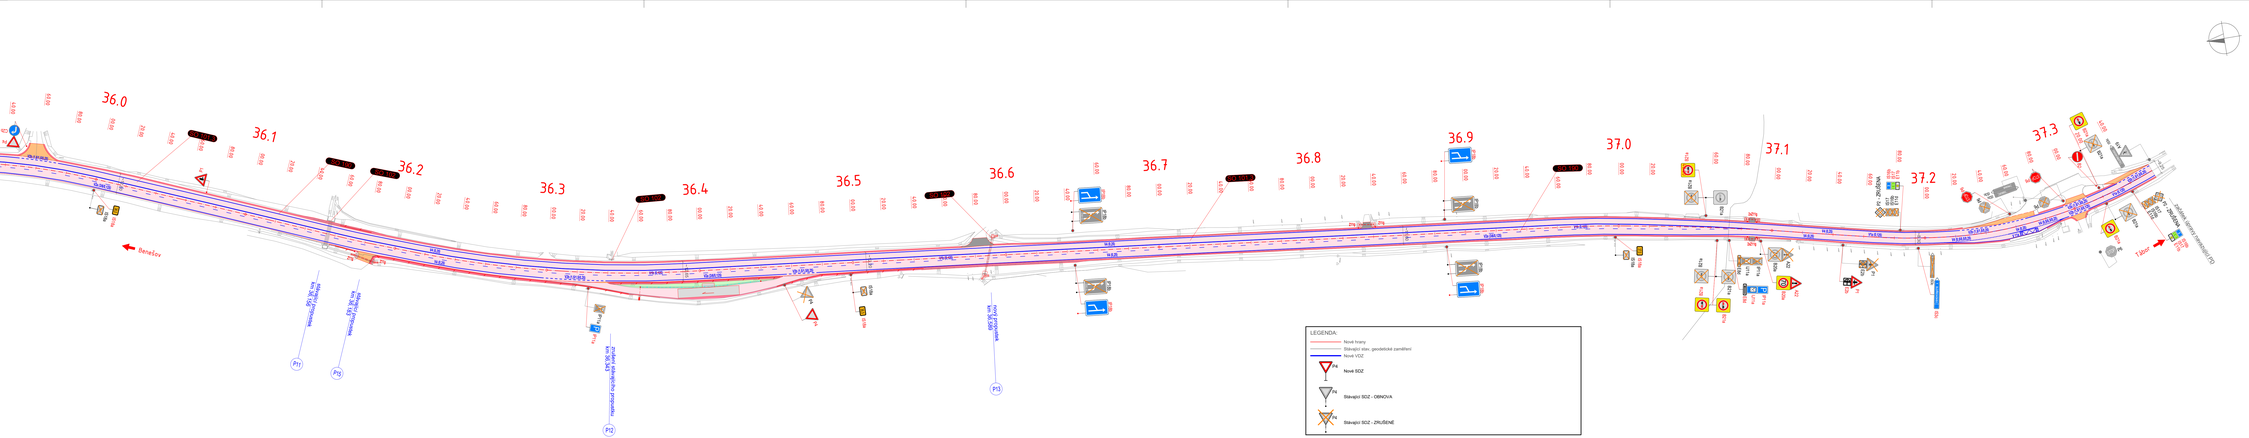

a			
b			
c			
d	text změny - odůvodnění	datum	podpis

Název stavby: I/3 Votice - Oldřichovec oprava povrchu a odvodnění komunikace	Číslo objektu: 190

Objednatel stavby: ŘEDITELSTVÍ SILNIC A DÁLNIC ŘEDITELSTVÍ SILNIC A DÁLNIC s. p. Čerčanská 2023/12, 140 00 Praha 4 - Kč	Zástupce: Kontroloval: Datum: Podpis:
Zhotovitel stavby: M - SILNICE M - SILNICE a.s. Husova 1697, Bílé Předměstí, 530 03 Pardubice	Zástupce: M - SILNICE a.s. Pardubice Husova 1697 530 03 Pardubice IČO: 46504146 Tel/fax/mail: 290321, 190 10 Praha 9 Kontroloval: Datum: Podpis:
Koordinátor RDS: M - PROJEKCE M - PROJEKCE s.r.o. Resslova 958/13, 500 02 Hradec Králové	Zástupce: Kontroloval: Datum: Podpis:

KONCEPT

Současnosový systém SJTSK, Výškový systém Bpv

Hlavní projektant: Karel Laška Podpis:	Odpovědný projektant: Karel Laška Podpis:	Generální ředitel: ING. PETR HÁJEK Ředitel závodu Liberec: ING. JIŘÍ EHRENBERGER	Zhotovitel: M - PROJEKCE M - PROJEKCE s.r.o. Resslova 958/13, 500 02 Hradec Králové
Technická kontrola: DAVID SENOHRABEK, DiS Podpis:	Hlavní inženýr projektu: Karel Laška Podpis:		

Kraj: STŘEDOČESKÝ KRAJ		Čís. zakázky:	26-024-02
Katast. úz.: Votice, Hostišov, Kouty u Smilkova		Čís. akce:	
Objednatel: M - SILNICE a.s., Husova 1697, Bílé Předměstí, 530 03 Pardubice		Datum:	03/2026
Objekt: **SO 190 Svislé s vodorovné dopravní značení v km 31,450 - 37,357**		Formát:	8x A4
		Měřítko:	1:1000
		Stupeň:	**RDS**
Příloha: **Situace dopravního značení Č.5**		Číslo přílohy:	**2.5**