

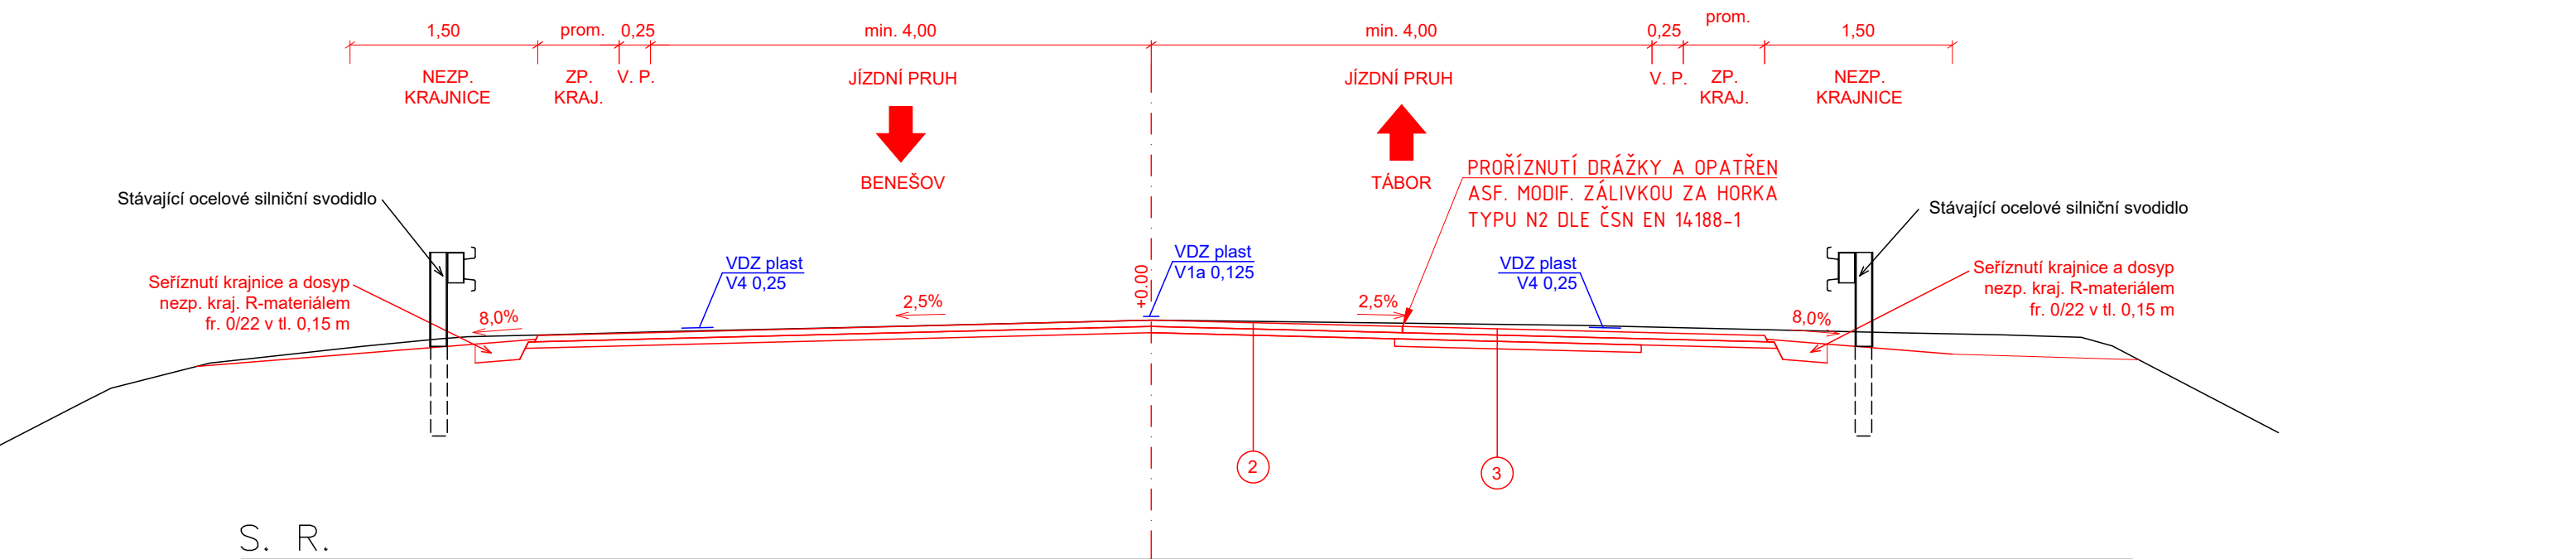


VZOROVÉ PŘÍČNÉ ŘEZY
M 1:50

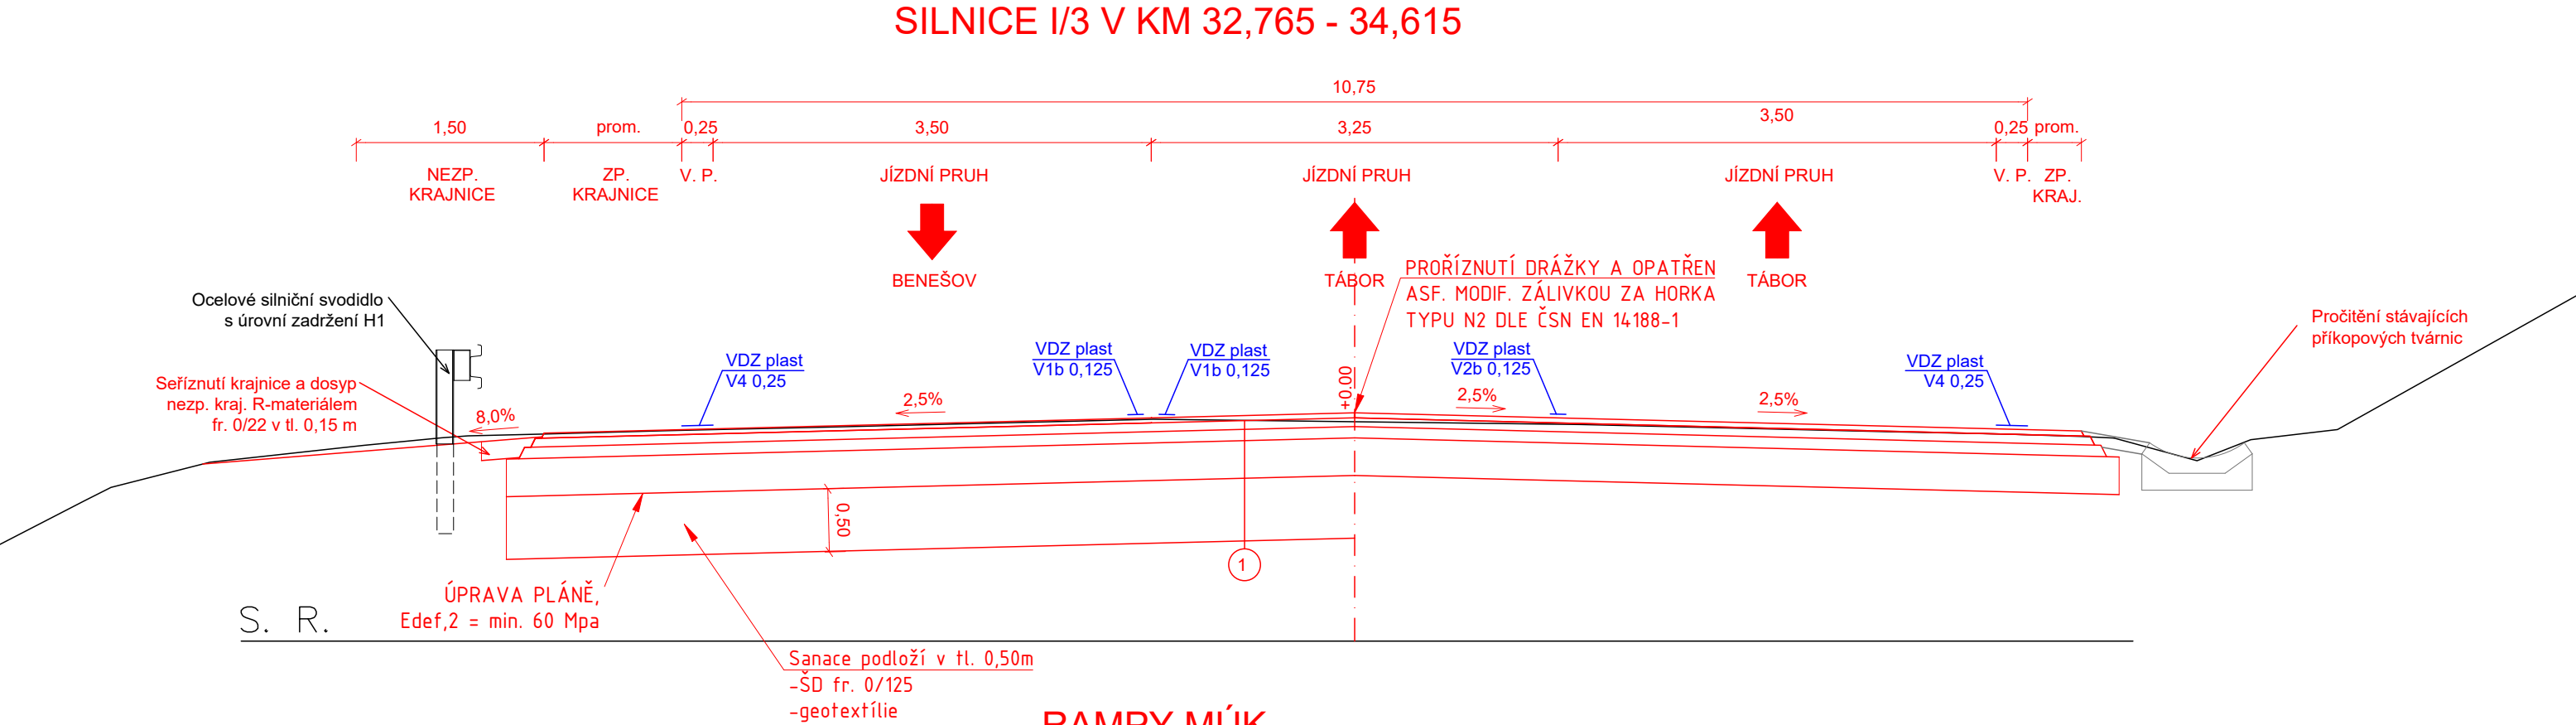

ŘEZ V MÍSTĚ NAPOJENÍ NA STÁVAJÍCÍ KOMUNIKACI

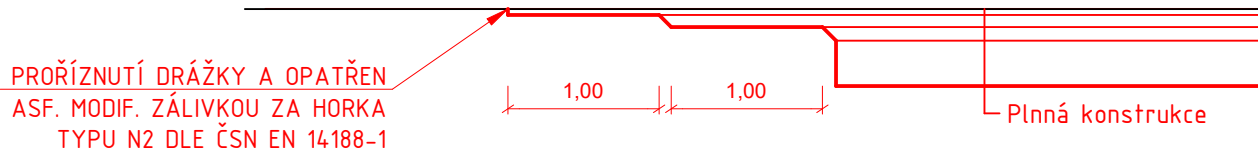

1	Frézování tl. 210mm			
	Asfaltový koberec mastixový modifikovaný s posypem predobalným kam. fr. 2/4	SMA 11 S	40 mm	ČSN EN 13108-5
	Spojovací postřik emulzní modifikovaný	PS-C	1,5 kg/m²	ČSN 73 6121
	Asfaltový beton pro ložné vrstvy modifikovaný	ACL 22 S	0,30 kg/m²	ČSN EN 13808, ČSN 73 6129
	Spojovací postřik emulzní modifikovaný	PS-C	80 mm	ČSN EN 13108-1, ČSN 73 6121
	Asfaltový beton pro ložné vrstvy modifikovaný	PS-C	0,30 kg/m²	ČSN EN 13808, ČSN 73 6129
	Asfaltová směs s vysokým modulem tuhosti Recyklace	VTM 22 PMB RS CA	90 mm	ČSN EN 13108-1, ČSN 73 6121
	Celkem		300 mm	ČSN 73 6147
			510 mm	▼ 150 MPa

2	Frézování tl. 120mm			
	Asfaltový koberec mastixový modifikovaný s posypem predobalným kam. fr. 2/4	SMA 11 S	40 mm	ČSN EN 13108-5
	Spojovací postřik emulzní modifikovaný	PS-C	1,5 kg/m²	ČSN 73 6121
	Asfaltový beton pro ložné vrstvy modifikovaný	ACL 22 S	0,30 kg/m²	ČSN EN 13808, ČSN 73 6129
	Spojovací postřik emulzní modifikovaný	PS-C	80 mm	ČSN EN 13108-1, ČSN 73 6121
	Celkem		120 mm	ČSN EN 13808, ČSN 73 6129

3	Frézování tl. 160mm (lokální oprava ACP - předpoklad 30% vozovky)			
	Asfaltový koberec mastixový modifikovaný s posypem predobalným kam. fr. 2/4	SMA 11 S	40 mm	ČSN EN 13108-5
	Spojovací postřik emulzní modifikovaný	PS-C	1,5 kg/m²	ČSN 73 6121
	Asfaltový beton pro ložné vrstvy modifikovaný	ACL 22 S	0,30 kg/m²	ČSN EN 13808, ČSN 73 6129
	Spojovací postřik emulzní modifikovaný	PS-C	80 mm	ČSN EN 13108-1, ČSN 73 6121
	Asfaltový beton pro ložné vrstvy modifikovaný	PS-C	0,30 kg/m²	ČSN EN 13808, ČSN 73 6129
	Asfaltový beton pro podkladní vrstvy	ACP 16S 50/70	60 mm	ČSN EN 13108-1, ČSN 73 6121
	Spojovací postřik emulzní modifikovaný	PS-C	0,30 kg/m²	ČSN EN 13808, ČSN 73 6129
	Celkem		180 mm	

Pro jednotlivé asfaltové vrstvy budou použity minimálně tyto pojiva:

SMA 11S modif. PMB 45/80-65
ACL 22S modif. PMB 25/55-65
VTM 22 modif. PMB 25/55-60
RS CA - s hydraulickým pojivem a asfaltovou emulzí, množství stanoví průkazná zkouška po odebrání materiálů.
ACO 11+ modif. PMB 45/80-65

Únosnost na vrstvě RS CA Edef,2 = 150 MPa.

a			
b			
c			
č.	text změny - odůvodnění	datum	podpis

Název stavby:	I/3 Votice - Oldřichovec oprava povrchu a odvodnění komunikace	Číslo objektu:	101.2 101.3
---------------	--	----------------	----------------

Objednatel stavby:	 ŘEDITELSTVÍ SILNIC A DÁLNIC Čerčanská 2023/12, 140 00 Praha 4 - Krč	Razítko:	
Kontroloval:		Datum:	Podpis:

Zhotovitel stavby:	 M - SILNICE a.s. Husova 1697, Bílé Předměstí, 530 03 Pardubice	Razítko:	 M - SILNICE a.s. Pardubice, Husova 1697 IČO 421 96 868 oblastní závod ÚHA - S. Trabantská 290/31, 190 15 Praha 9
Kontroloval:		Datum:	Podpis:

Koordinátor RDS:	 M - PROJEKCE s.r.o. Resslova 956/13, 500 02 Hradec Králové	Razítko:	
Kontroloval:		Datum:	Podpis:

ČISTOPIS

Souřadnicový systém S-JTSK, Výškový systém BpV			
Navrhl/vypracoval:	Zodpovědný projektant:	Generální ředitel:	Zhotovitel:
Karel Láska	Karel Láska	ING. PETR HÁJEK	
Podpis:	Podpis:	Ředitel ateliéru Liberec:	M - PROJEKCE s.r.o. Resslova 956/13, 500 02 Hradec Králové
Technická kontrola:	Hlavní inženýr projektu:	ING. JIŘÍ EHRENBARGER	
DAVID SENOHRÁBEK, DIS	Karel Láska		
Podpis:	Podpis:		

Kraj:	STŘEDOČESKÝ KRAJ	Čís. zakázky:	26-024-02
Katastr. úz.:	Votice, Hostišov, Kouty u Smilkova	Čís. akce:	-
Objednatel:	M - SILNICE a.s., Husova 1697, Bílé Předměstí, 530 03 Pardubice	Datum:	04/2026
Objekt:	SO 101.2 - Oprava silnice I/3 v km 32,765 - 34,615 SO 101.3 - Oprava silnice I/3 v km 34,615 - 37,357	Formát:	4x A4
		Měřítko:	1:50
		Stupeň:	RDS
Příloha:	Vzorové příčné řezy SO 101.2	Čís. přílohy:	4.1