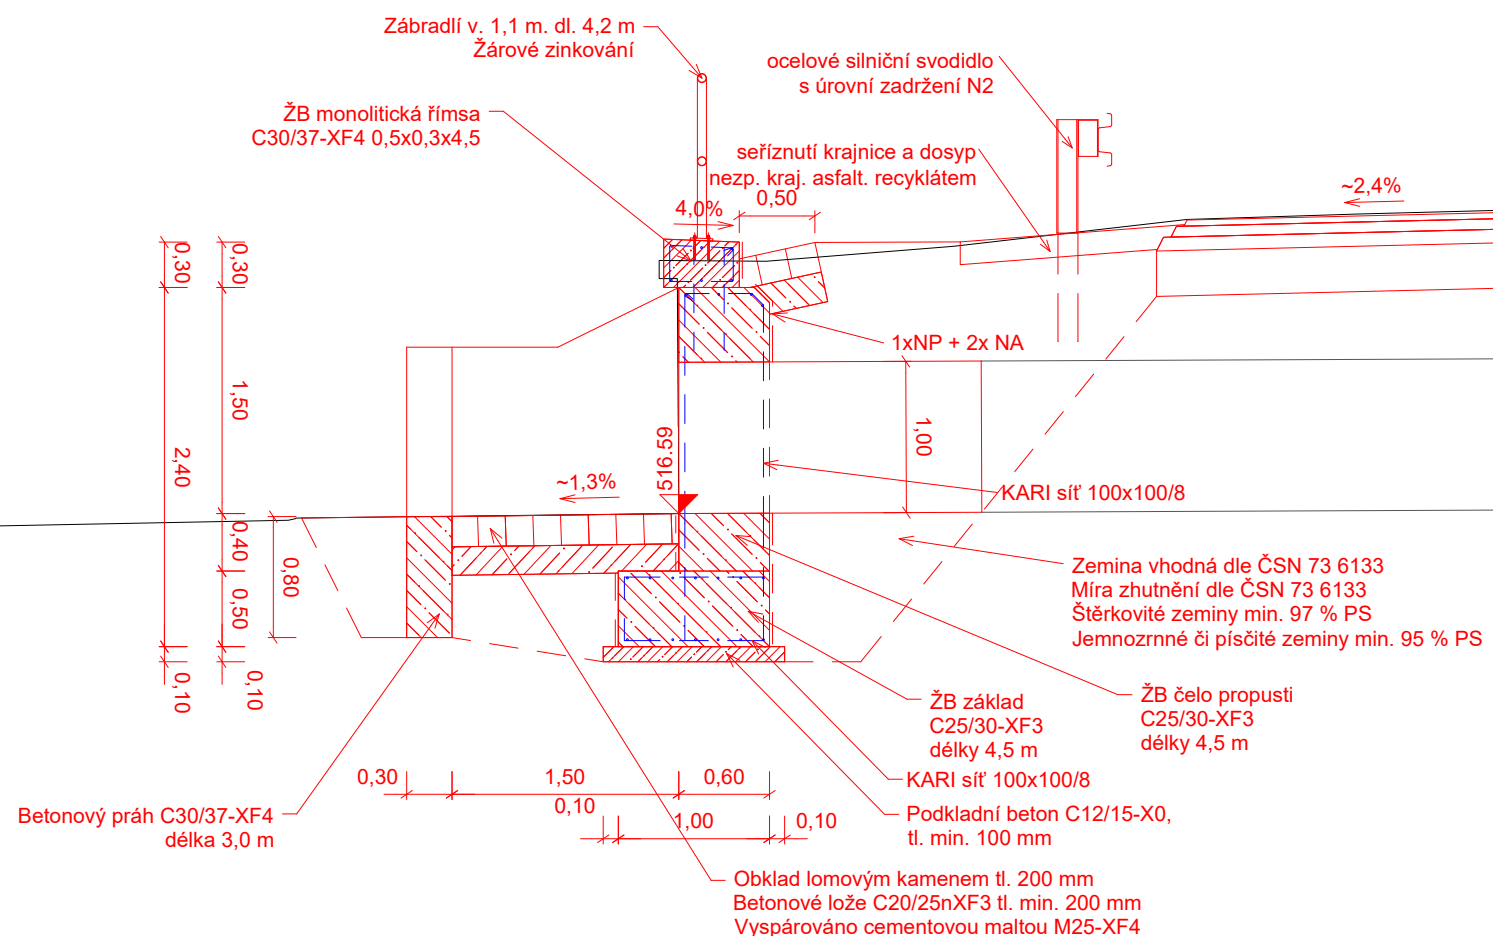


M 1:50



513,0

POZNÁMKA:
Čelo a základ propustku jsou vyztuženy KARI sítí 100x100/8 při povrchu.
Římsa je vyztužena viz vzor vyztužení římsy za technickou zprávou.
Mezi KARI sítěmi v základu bude umístěn distanční kozlík z betonářské vyztuže v rozteči 900 - 1200 mm.

 
 
a			
b			
c			
č.	text změny - odůvodnění	datum	podpis
Název stavby: I/3 Votice - Oldřichovec oprava povrchu a odvodnění komunikace		Číslo objektu: 102	

Objednatel stavby:  ŘEDITELSTVÍ SILNIC A DÁLNIC ŘEDITELSTVÍ SILNIC A DÁLNIC s. p. Čerčanská 2023/12, 140 00 Praha 4 - Krč	Razítko: Kontroloval: Datum: Podpis:
---	---

Zhotovitel stavby:  M - SILNICE a.s. Husova 1697, Bílé Předměstí, 530 03 Pardubice	Razítko:  Kontroloval: Datum: Podpis:
--	--

Koordinátor RDS:  M - PROJEKCE M - PROJEKCE s.r.o. Resslova 956/13, 500 02 Hradec Králové	Razítko: Kontroloval: Datum: Podpis:
---	---

ČISTOPIS

Souřadnicový systém S-JTSK, Výškový systém Bpv			
Navrhl/vypracoval: Karel Láska Podpis: 	Zodpovědný projektant: Karel Láska Podpis: 	Generální ředitel: ING. PETR HÁJEK	Zhotovitel:  M - PROJEKCE
Technická kontrola: DAVID SENOHRÁBEK, DiS Podpis: 	Hlavní inženýr projektu: Karel Láska Podpis: 	Ředitel ateliéru Liberec: ING. JIŘÍ EHRENBARGER	M - PROJEKCE s.r.o. Resslova 956/13, 500 02 Hradec Králové

Kraj: STŘEDOČESKÝ KRAJ	Čís. zakázky:	26-024-02
Katastr. úz.: Votice, Hostišov, Kouty u Smilkova	Čís. akce:	-
Objednatel: M - SILNICE a.s., Husova 1697, Bílé Předměstí, 530 03 Pardubice	Datum:	04/2026
Objekt: SO 102 Oprava propustků	Formát:	2x A4
	Měřítko:	1:50
	Stupeň: RDS	Souprava:
Příloha: Propustek v km 33,377	Čís. přílohy: 2.2	