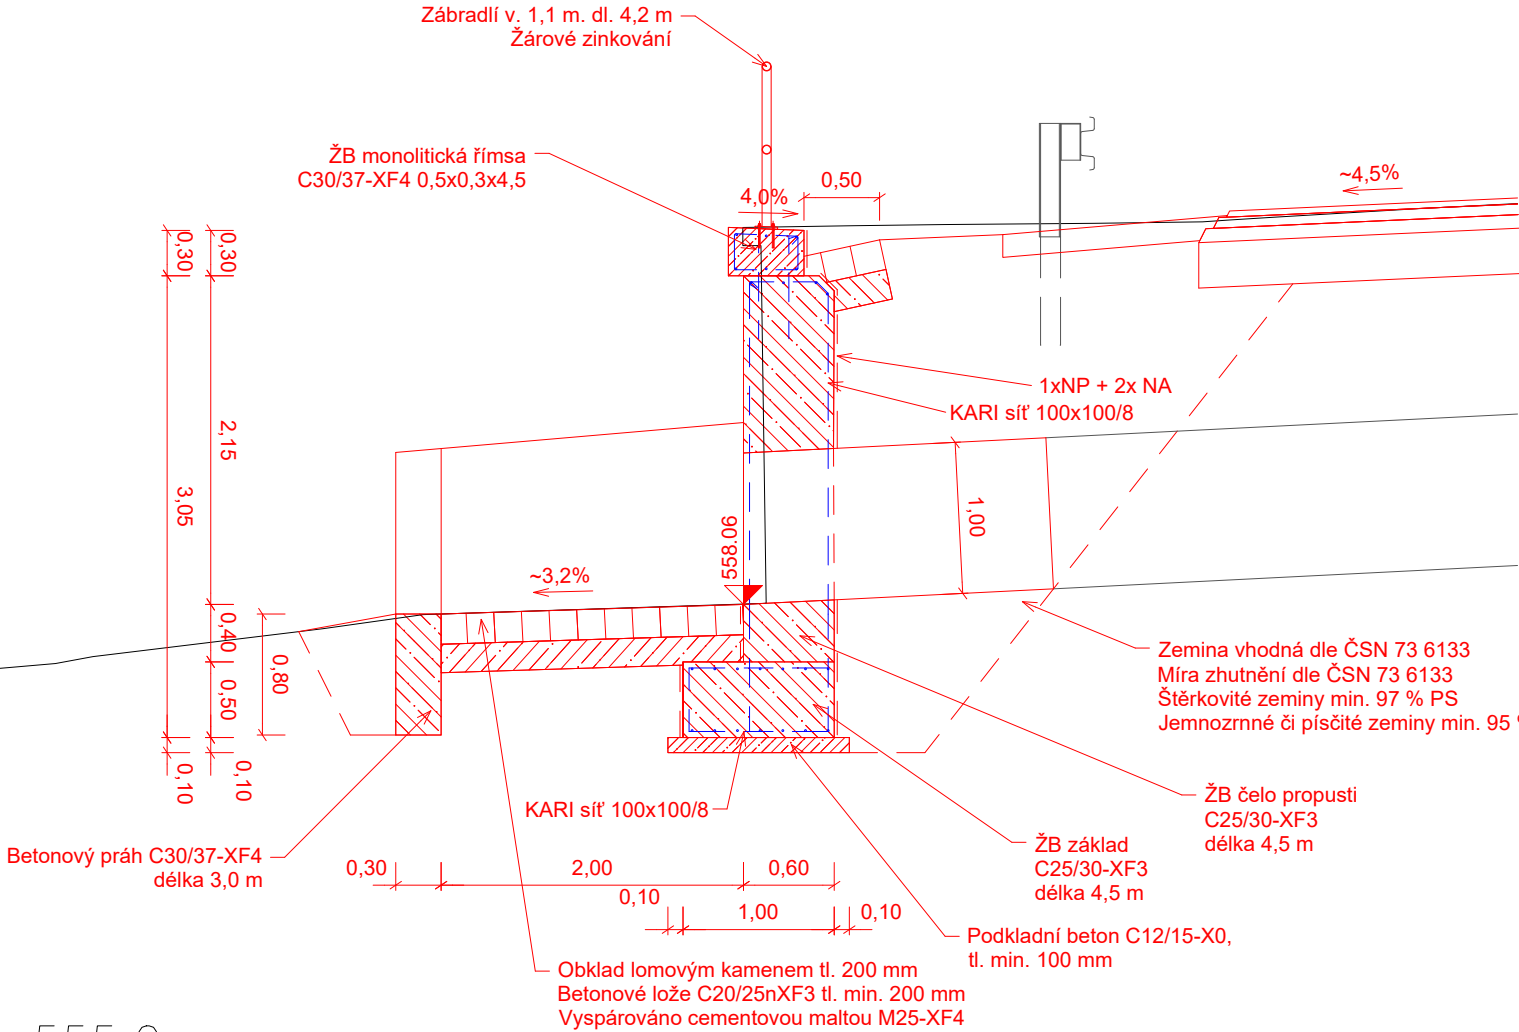


OPRAVA PROPUSTKU KM 34,229

M 1:50

ČELO NA VÝTOKU PROPUSTKU (P4)



555,0

POZNÁMKA:
Čelo a základ propustku jsou vyztuženy KARI sítí 100x100/8 při povrchu.
Římsa je vyztužena viz vzor vyztužení římsy za technickou zprávou.
Mezi KARI sítěmi v základu bude umístěn distanční kozlík z betonářské výztuže v rozteči 900 - 1200 mm.

a			
b			
c			
č.	text změny - odůvodnění	datum	podpis

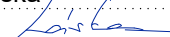
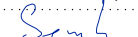
Název stavby: I/3 Votice - Oldřichovec oprava povrchu a odvodnění komunikace	Číslo objektu: 102
---	---------------------------

Objednatel stavby:  ŘEDITELSTVÍ SILNIC A DÁLNIC s. p. Čerčanská 2023/12, 140 00 Praha 4 - Krč	Razítko: Kontroloval: Datum: Podpis:
--	--

Zhotovitel stavby:  M - SILNICE a.s. Husova 1697, Bílé Předměstí, 530 03 Pardubice	Razítko:  Kontroloval: Datum: Podpis:
---	---

Koordinátor RDS:  M - PROJEKCE s.r.o. Resslova 956/13, 500 02 Hradec Králové	Razítko: Kontroloval: Datum: Podpis:
--	--

ČISTOPIS

Souřadnicový systém S-JTSK, Výškový systém Bpv			
Navrhl/vypracoval: Karel Láska Podpis: 	Zodpovědný projektant: Karel Láska Podpis: 	Generální ředitel: ING. PETR HÁJEK Ředitel ateliéru Liberec:	Zhotovitel:  M - PROJEKCE s.r.o. Resslova 956/13, 500 02 Hradec Králové
Technická kontrola: DAVID SENOHRÁBEK, DiS Podpis: 	Hlavní inženýr projektu: Karel Láska Podpis: 	ING. JIŘÍ EHRENBARGER	

Kraj: STŘEDOČESKÝ KRAJ	Čís. zakázky: 26-024-02
Katastr. úz.: Votice, Hostišov, Kouty u Smilkova	Čís. akce: -
Objednatel: M - SILNICE a.s., Husova 1697, Bílé Předměstí, 530 03 Pardubice	Datum: 04/2026
Objekt: SO 102 Oprava propustků	Formát: 2x A4
	Měřítko: 1:50
	Stupeň: RDS
	Souprava:
Příloha: Propustek v km 34,229	Čís. přílohy: 2.4