


OPRAVA PROPUSTKU KM 35,592

M 1:50

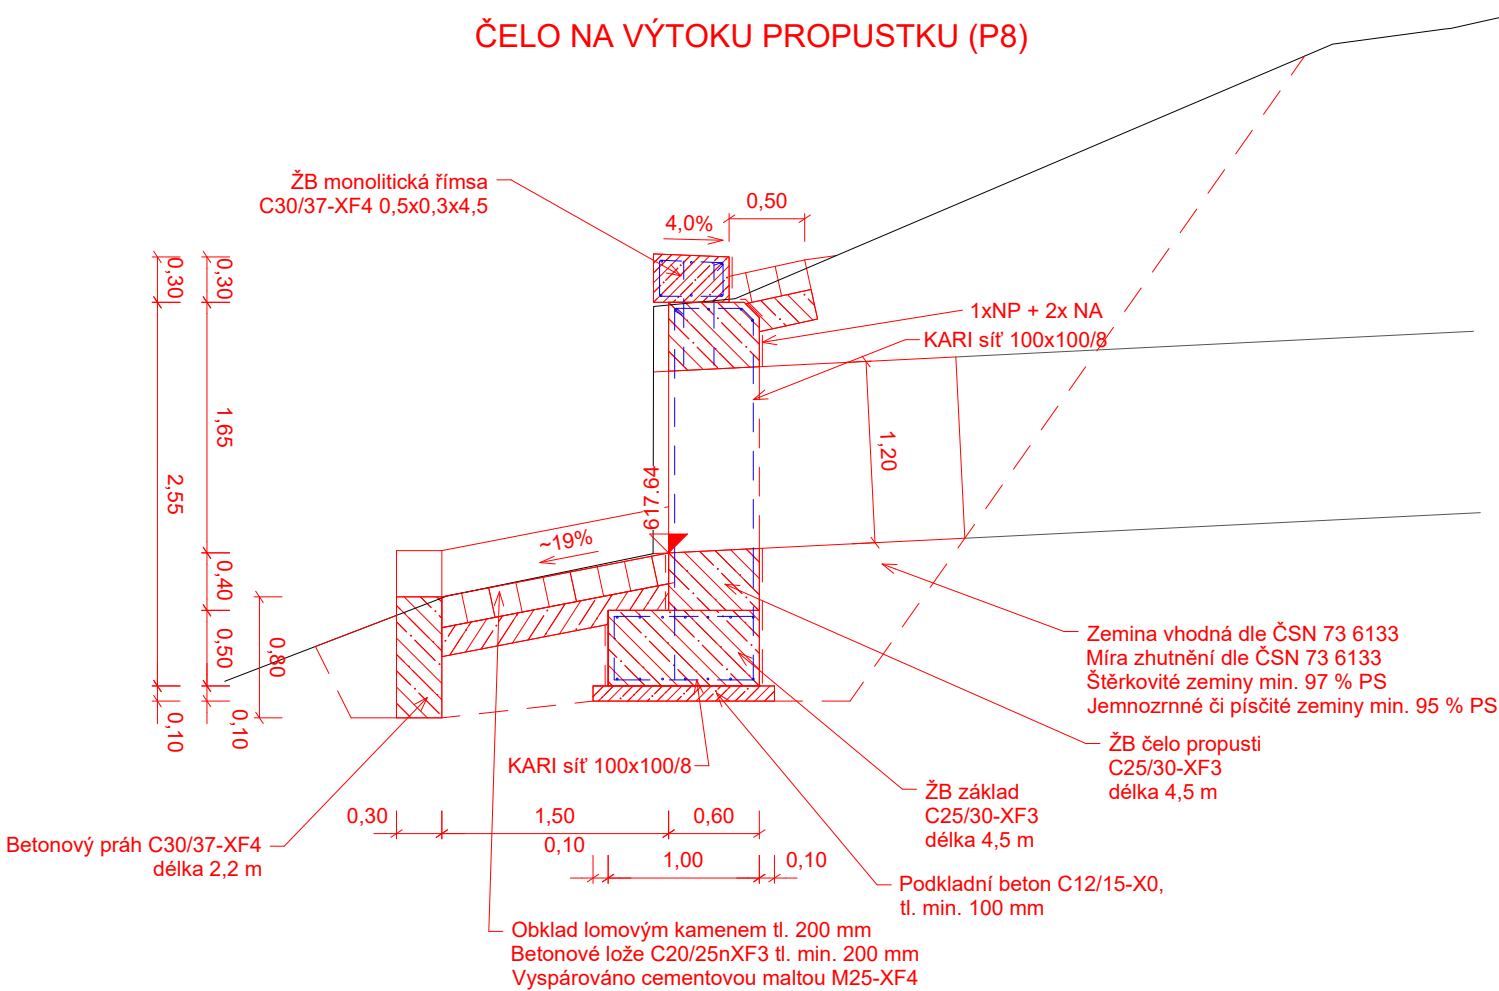

614,0

**POZNÁMKA:**  
Čelo a základ propustku jsou vyztuženy KARI sítí 100x100/8 při povrchu. Římsa je vyztužena viz vzor vyztužení římsy za technickou zprávou. Mezi KARI sítěmi v základu bude umístěn distanční kozlík z betonářské výztuže v rozteči 900 - 1200 mm.

|    |                         |       |        |
|----|-------------------------|-------|--------|
| a  |                         |       |        |
| b  |                         |       |        |
| c  |                         |       |        |
| č. | text změny - odůvodnění | datum | podpis |


|                                                                                     |                           |
|-------------------------------------------------------------------------------------|---------------------------|
| Název stavby: <b>I/3 Votice - Oldřichovec oprava povrchu a odvodnění komunikace</b> | Číslo objektu: <b>102</b> |
|-------------------------------------------------------------------------------------|---------------------------|

|   |                                                |
|---|------------------------------------------------|
| Objednatel stavby:<br><br><b>ŘEDITELSTVÍ SILNIC A DÁLNIC s. p.</b><br>Čerčanská 2023/12, 140 00 Praha 4 - Krč | Razítko:<br><br>Kontroloval:<br>Datum: Podpis: |
|---|------------------------------------------------|

|   |   |
|---|---|
| Zhotovitel stavby:<br><br><b>M - SILNICE a.s.</b><br>Husova 1697, Bílé Předměstí, 530 03 Pardubice | Razítko:<br><br>Kontroloval:<br>Datum: Podpis: |
|---|---|

|   |                                                |
|---|------------------------------------------------|
| Koordinátor RDS:<br><br><b>M - PROJEKCE s.r.o.</b><br>Resslova 956/13, 500 02 Hradec Králové | Razítko:<br><br>Kontroloval:<br>Datum: Podpis: |
|---|------------------------------------------------|

ČISTOPIS
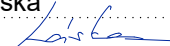
|   |   |                                                                           |   |
|---|---|---------------------------------------------------------------------------|---|
| Souřadnicový systém S-JTSK, Výškový systém Bpv   |   |                                                                           |   |
| Navrhl/vypracoval:<br><b>Karel Láška</b><br>Podpis:             | Zodpovědný projektant:<br><b>Karel Láška</b><br>Podpis:    | Generální ředitel:<br><b>ING. PETR HÁJEK</b><br>Ředitel ateliéru Liberec: | Zhotovitel:<br><br><b>M - PROJEKCE s.r.o.</b><br>Resslova 956/13, 500 02 Hradec Králové |
| Technická kontrola:<br><b>DAVID SENOHRÁBEK, DiS</b><br>Podpis:  | Hlavní inženýr projektu:<br><b>Karel Láška</b><br>Podpis:  | ING. JIŘÍ EHRENBARGER                                                     |   |

|                                                                             |                                 |
|-----------------------------------------------------------------------------|---------------------------------|
| Kraj: STŘEDOČESKÝ KRAJ                                                      | Čís. zakázky: 26-024-02         |
| Katastr. úz.: Votice, Hostišov, Kouty u Smilkova                            | Čís. akce: -                    |
| Objednatel: M - SILNICE a.s., Husova 1697, Bílé Předměstí, 530 03 Pardubice | Datum: 04/2026                  |
| Objekt: <b>SO 102</b><br><b>Oprava propustků</b>                            | Formát: 2x A4                   |
| Příloha: <b>Propustek v km 35,592</b>                                       | Měřítko: 1:50                   |
|                                                                             | Stupeň: <b>RDS</b><br>Souprava: |
|                                                                             | Čís. přílohy: <b>2.6</b>        |