

KATASTRÁLNÍ ÚZEMÍ
OKRES:
KRAJ:

Vošice [785041]
Benešov
CZ 020 Středočeský

Hostišov [615251]
Benešov
CZ 020 Středočeský

BENEŠOV

TÁBOR

SKLONOVÉ POMĚRY:

MĚŘÍTKA:
1:1000, 1:100

KÓTY NIVELTY:


KÓTY TERÉNU:

SGVNÁVACÍ ROVINA:

STANIČNÍ:

VZDÁLENOST PŘ. ŘEZO:

SMĚROVÉ POMĚRY:



a			
b			
c	text změny - odůvodnění	datum	podpis
Název stavby: I/3 Vošice - Oldřichovec oprava povrchu a odvodnění komunikace		Číslo objektu: 101.2	101.3
Objednatel stavby: ŘEDITELSTVÍ SILNIC A DÁLNIC ŘEDITELSTVÍ SILNIC A DÁLNIC s. p. Čerčanská 2023/12, 140 00 Praha 4 - Krč		Razítko:	Kontrolovat: Datum: Podpis:
Zhotovitel stavby: M - SILNICE a.s. Pardubice, Husova 1697 IČO 421 96 868 Tržní ulice 200/1, 190 15 Tržeb		Razítko:	Kontrolovat: Datum: Podpis:
Koordínátor RDS: M - PROJEKCE s.r.o. Resslova 956/13, 500 02 Hradec Králové		Razítko:	Kontrolovat: Datum: Podpis:

ČISTOPIS

Hlavní/výpracoval: Karel Láska Podpis: [Signature] Technická kontrola: DAVID ŠENOURABEK, DIS Podpis: [Signature]		Zodpovědný projektant: Karel Láska Podpis: [Signature] Hlavní inženýr projektu: Karel Láska Podpis: [Signature]		Souřadnicový systém S-JTSK, Výškový systém bvp Generální redaktor: ING. PETR HÁJEK Redaktor atelieru Liberec: Karel Láska Podpis: [Signature]		Zhotovitel: M - PROJEKCE s.r.o. Resslova 956/13, 500 02 Hradec Králové	
Kraj: STŘEDOČESKÝ KRAJ Katastr. úz.: Vošice, Hostišov, Kouty u Smilčova Objednatel: M - SILNICE a.s., Husova 1697, Bílé Předměstí, 530 03 Pardubice Měřítko: 1:1000/100 Průřez: Podélný profil č. 1		Čís. zakázky: 26-024-02 Čís. akce: 04/2026 Datum: 18x A4 Formát: 1:1000/100 Suprava: RDS		Čís. přílohy: 3.1			