

KATASTRÁLNÍ ÚZEMÍ
OKRES:
KRAJ:


Hostišov [615251]
Benešov
CZ 020 Středočeský

Kouty u Smilkova [750956]
Benešov
CZ 020 Středočeský

BENEŠOV

TÁBOR

SKLONOVÉ POMĚRY:



a			
b			
c			
č	text změny - odůvodnění	datum	podpis
Název stavby: I/3 Votice - Oldřichovec oprava povrchu a odvodnění komunikace		Číslo objektu: 101.2	101.3
Objednatel stavby: ŘEDITELSTVÍ SILNICE A DÁLNIC s.p. Čertánská 2023/12, 140 00 Praha 4 - Krč		Razisko:	Kontroloval: Datum: Podpis:
Zhotovitel stavby: M - SILNICE a.s. Pardubice, Habova 1697 IČO 421 86 868		Razisko:	Kontroloval: Datum: Podpis:
Koordínátor RDS: M - PROJEKCE s.r.o. Reslovka 956/13, 500 02 Hradec Králové		Razisko:	Kontroloval: Datum: Podpis:

ČISTOPIS

Hlavní vypracoval: Karel Láska		Zodpovědný projektant: Karel Láska	Generální redaktor: ING. PETR HÁJEK	Souřadnicový systém S-JTSK	Výškový systém Bpv
Podpis: [Signature]		Podpis: [Signature]	Podpis: [Signature]		
Technická kontrola: DAVID SENOHRÁBEK, DIS		Hlavní inženýr projektu: Karel Láska	Redaktor: ING. JAROSLAV LIBEREC		
Podpis: [Signature]		Podpis: [Signature]	Podpis: [Signature]		
Kraj: STŘEDOČESKÝ KRAJ		Katastr. úz.: Votice, Hostišov, Kouty u Smilkova	Období: M - SILNICE a.s., Husova 1697, Bílé Předměstí, 530 03 Pardubice	Čís. zakázky: 26-024-02	
Objekt: SO 101.2 - Oprava silnice I/3 v km 32,765 - 34,615				Datum: 04/2026	
Formát: 18x A4				Stupeň: 1:1000/100	
Priloha: Podélný profil č.3				RDS	
				Čís. přílohy: 3.3	