


KATASTRÁLNÍ ÚZEMÍ:
OKRES:
KRAJ:

Kouty u Smilkova [750956]
Benešov
CZ 020 Středočeský

SKLONOVÉ POMĚRY:

← BENEŠOV

TÁBOR →

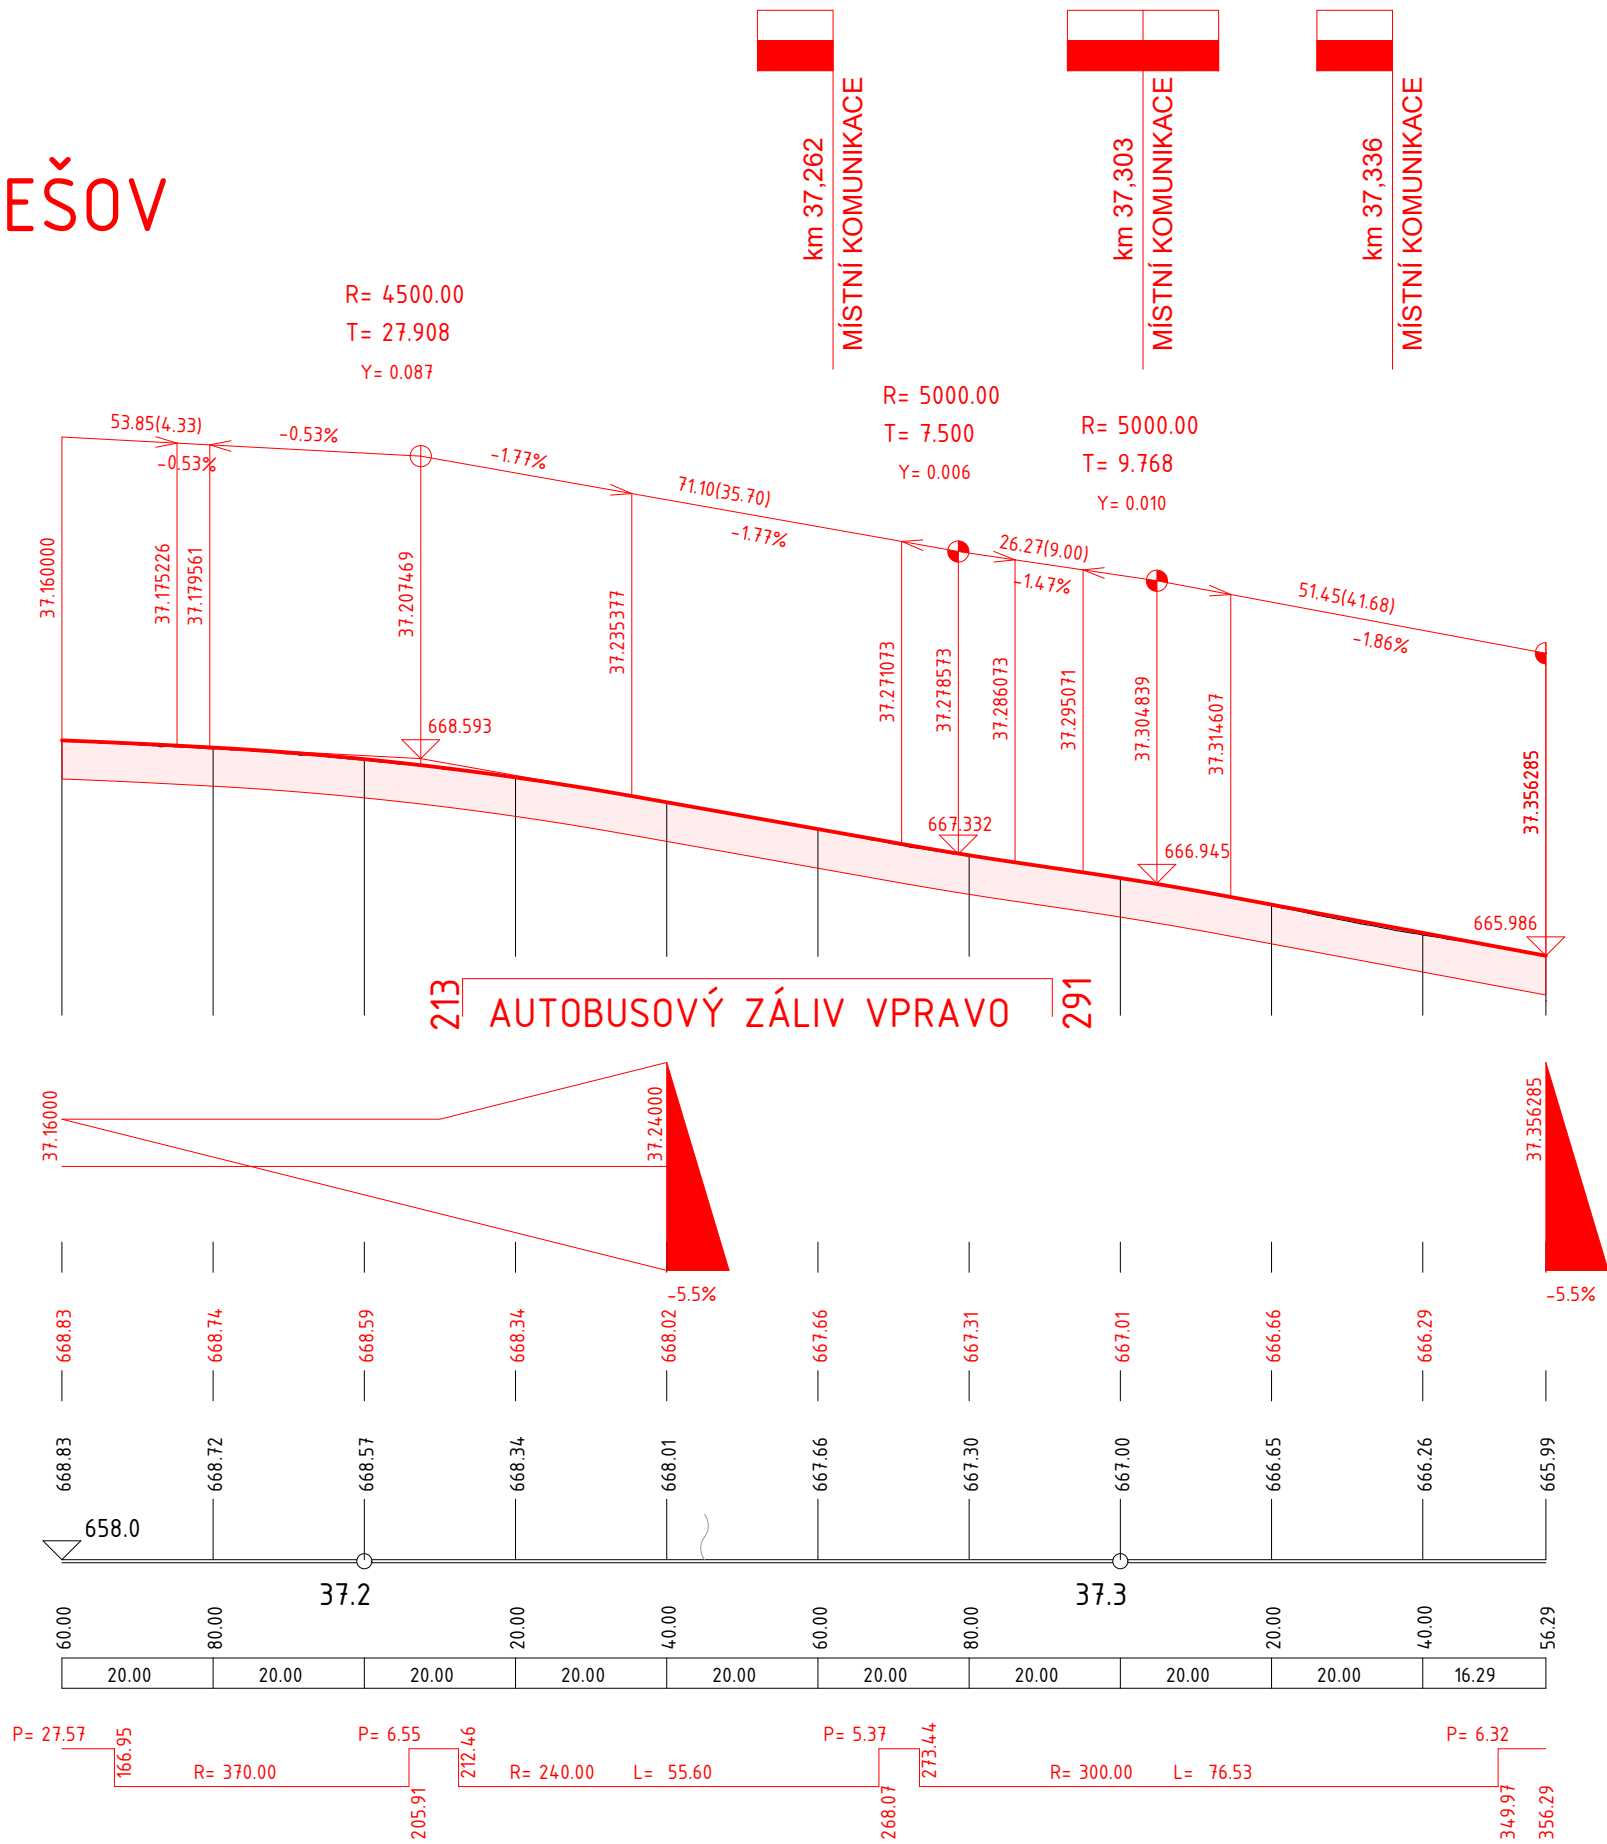

MĚŘÍTKA:
1: 1000., 1: 100.

KÓTY NIVELETY:

KÓTY TERÉNU:

SROVNÁVACÍ ROVINA:

STANIČENÍ:

VZDÁLENOST PŘ. ŘEZŮ:

SMĚROVÉ POMĚRY:

a			
b			
c			
č.	text změny - odůvodnění	datum	podpis

Název stavby: I/3 Votice - Oldřichovec oprava povrchu a odvodnění komunikace	Číslo objektu: 101.2 101.3
---	---

Objednatel stavby: ŘEDITELSTVÍ SILNIC A DÁLNIC s. p. Čerčanská 2023/12, 140 00 Praha 4 - Krč	Razítko: Kontroloval: Datum: Podpis:
---	--

Zhotovitel stavby: M - SILNICE a.s. Husova 1697, Bílé Předměstí, 530 03 Pardubice	Razítko: Kontroloval: Datum: Podpis:
--	--

Koordinátor RDS: M - PROJEKCE s.r.o. Resslova 956/13, 500 02 Hradec Králové	Razítko: Kontroloval: Datum: Podpis:
--	--

ČISTOPIS

Souřadnicový systém S-JTSK, Výškový systém Bpv			
Navrhl/vypracoval: Karel Láska Podpis:	Zodpovědný projektant: Karel Láska Podpis:	Generální ředitel: ING. PETR HÁJEK Ředitel ateliéru Liberec:	Zhotovitel: M - PROJEKCE s.r.o. Resslova 956/13, 500 02 Hradec Králové
Technická kontrola: DAVID SENOHRÁBEK, DiS Podpis:	Hlavní inženýr projektu: Karel Láska Podpis:	ING. JIŘÍ EHRENBARGER	

Kraj: STŘEDOČESKÝ KRAJ	Čís. zakázky:	26-024-02
Katastr. úz.: Votice, Hostišov, Kouty u Smilkova	Čís. akce:	-
Objednatel: M - SILNICE a.s., Husova 1697, Bílé Předměstí, 530 03 Pardubice	Datum:	04/2026
Objekt: SO 101.2 - Oprava silnice I/3 v km 32,765 - 34,615 SO 101.3 - Oprava silnice I/3 v km 34,615 - 37,357	Formát:	18x A4
	Měřítko:	1:1000/100
	Stupeň:	RDS Souprava:
Příloha:	Čís. přílohy:	
Podélný profil č.4		3.4