


SITUACE STAVBY SO 101
M 1:1000



a			
b			
c			
č	text změny - odůvodnění	datum	podpis

Název stavby: I/3 Votice - Oldřichovec oprava povrchu a odvodnění komunikace	Číslo objektu: 101.1
---	-----------------------------

Objednatel stavby:  ŘEDITELSTVÍ SILNIC A DÁLNIC ŘEDITELSTVÍ SILNIC A DÁLNIC s. p. Čerčanská 2023/12, 140 00 Praha 4 - Krč	Razítko: Kontrolováno: Datum: Podpis:
--	---

Zhotovitel stavby:  M-SILNICE M - SILNICE a.s. Husova 1697, Bílé Předměstí, 530 03 Pardubice	Razítko: M - SILNICE a.s. Pardubice, Husova 1697 IČO 421 96 868 Ibažijní závod úřh 5- Trávníčská 2900/1, 100 15 Praha 9
---	---

Koordinátor RDS:  M - PROJEKCE M - PROJEKCE s.r.o. Resslova 956/13, 500 02 Hradec Králové	Razítko: Kontrolováno: Datum: Podpis:
--	---

Návrh/ Vypracoval: Karel Láška Podpis: <i>[Signature]</i>		Zodpovědný projektant: Karel Láška Podpis: <i>[Signature]</i>		Generální řešitel: ING PETR HÁJEK Ředitel ateliéru Liberec: ING JIŘÍ EHRENBERGER		 M - PROJEKCE M - PROJEKCE s.r.o. Ressova 956/13, 500 02 Hradec Králové	
Souladníkový systém S-JTSK, Výškový systém Bpv		Zhotovitel:					
Technická kontrola: DAVID SENOHŘÁBEK, DIŠ Podpis: <i>[Signature]</i>		Hlavní inženýr projektu: Karel Láška Podpis: <i>[Signature]</i>					
Kraj: STŘEDOČESKÝ KRAJ Katastr. úz.: Votice Objednatel: M - SILNICE a.s., Husova 1697, Bílé Předměstí, 530 03 Pardubice Objekt:				Čís. zakázky: 26-024-02 Čís. skce: - Datum: 04/2026 Formát: A4 Měřítko: 1:1000 Stupeň:			
SO 101.1 Oprava silnice I/3 v km 31,450 - 32,765				RDS Souprava:			
Příloha:				Čís. přílohy:			
Situace				2.			