


SITUACE STAVBY SO 101
M 1:1000



a				
b				
c				
č.	text změny - odůvodnění	datum	podpis	
Název stavby: 1/3 Votice - Oldřichovec oprava povrchu a odvodnění komunikace		Číslo objektu:	101.2 101.3	
Objednatel stavby:  ŘEDITELSTVÍ SILNIC A DÁLNIC ŘEDITELSTVÍ SILNIC A DÁLNIC s. p. Čerčanská 2023/12, 140 00 Praha 4 - Krč		Razítko: Kontroloval: Datum:	Podpis:	
Zhotovitel stavby:  M - SILNICE M - SILNICE a.s. Husova 1697, Bílé Předměstí, 530 03 Pardubice		Razítko: M - SILNICE a.s. Pardubice, Husova 1697 IČO 421 96 668 Izbařská záhrada UH. 5 Trabantská 2803/1, 190 15 Praha 9	Kontroloval: Datum:	Podpis:
Koordinátor RDS:  M - PROJEKCE M - PROJEKCE s.r.o. Resslova 956/13, 500 02 Hradec Králové		Razítko: Kontroloval: Datum:	Podpis:	

ČISTOPIS

Navrh/Vypracoval: Karel Láska Podpis: <i>[Signature]</i>		Zodpovědný projektant: Karel Láska Podpis: <i>[Signature]</i>		Generální řešitel: ING. PETR HÁJEK Ředitel atelieru Liberec: ING. JIŘÍ EHRENBERGER		Souhradníkový systém S-JTSK, Výchový systém Bp Zhotovitel:	
Technická kontrola: DAVID SENOHŘÁBEK, DIS Podpis: <i>[Signature]</i>		Hlavní inženýr projektu: Karel Láska Podpis: <i>[Signature]</i>				M - PROJEKT s.r.o. Resslova 956/13, 500 02 Hradec Králové	
Kraj: STŘEDOČESKÝ KRAJ						Čís. zakázky: 26-024-02	
Katastr úz.: Votice, Hostišov, Kouty u Smilкова						Čís. akce:	
Objednatel: M - SILNICE a.s., Husova 1697, Bílé Předměstí, 530 03 Pardubice						Datum: 04/2026	
Objekt:						Formát: 8x A4	
SO 101.2 - Oprava silnice I/3 v km 32,765 - 34,615						Měřítko: 1:1000	
SO 101.3 - Oprava silnice I/3 v km 34,615 - 37,357						Stupeň:	
Příloha:						Čís. přílohy:	
Situace č. 1						RDS	
2.1						2.1	