


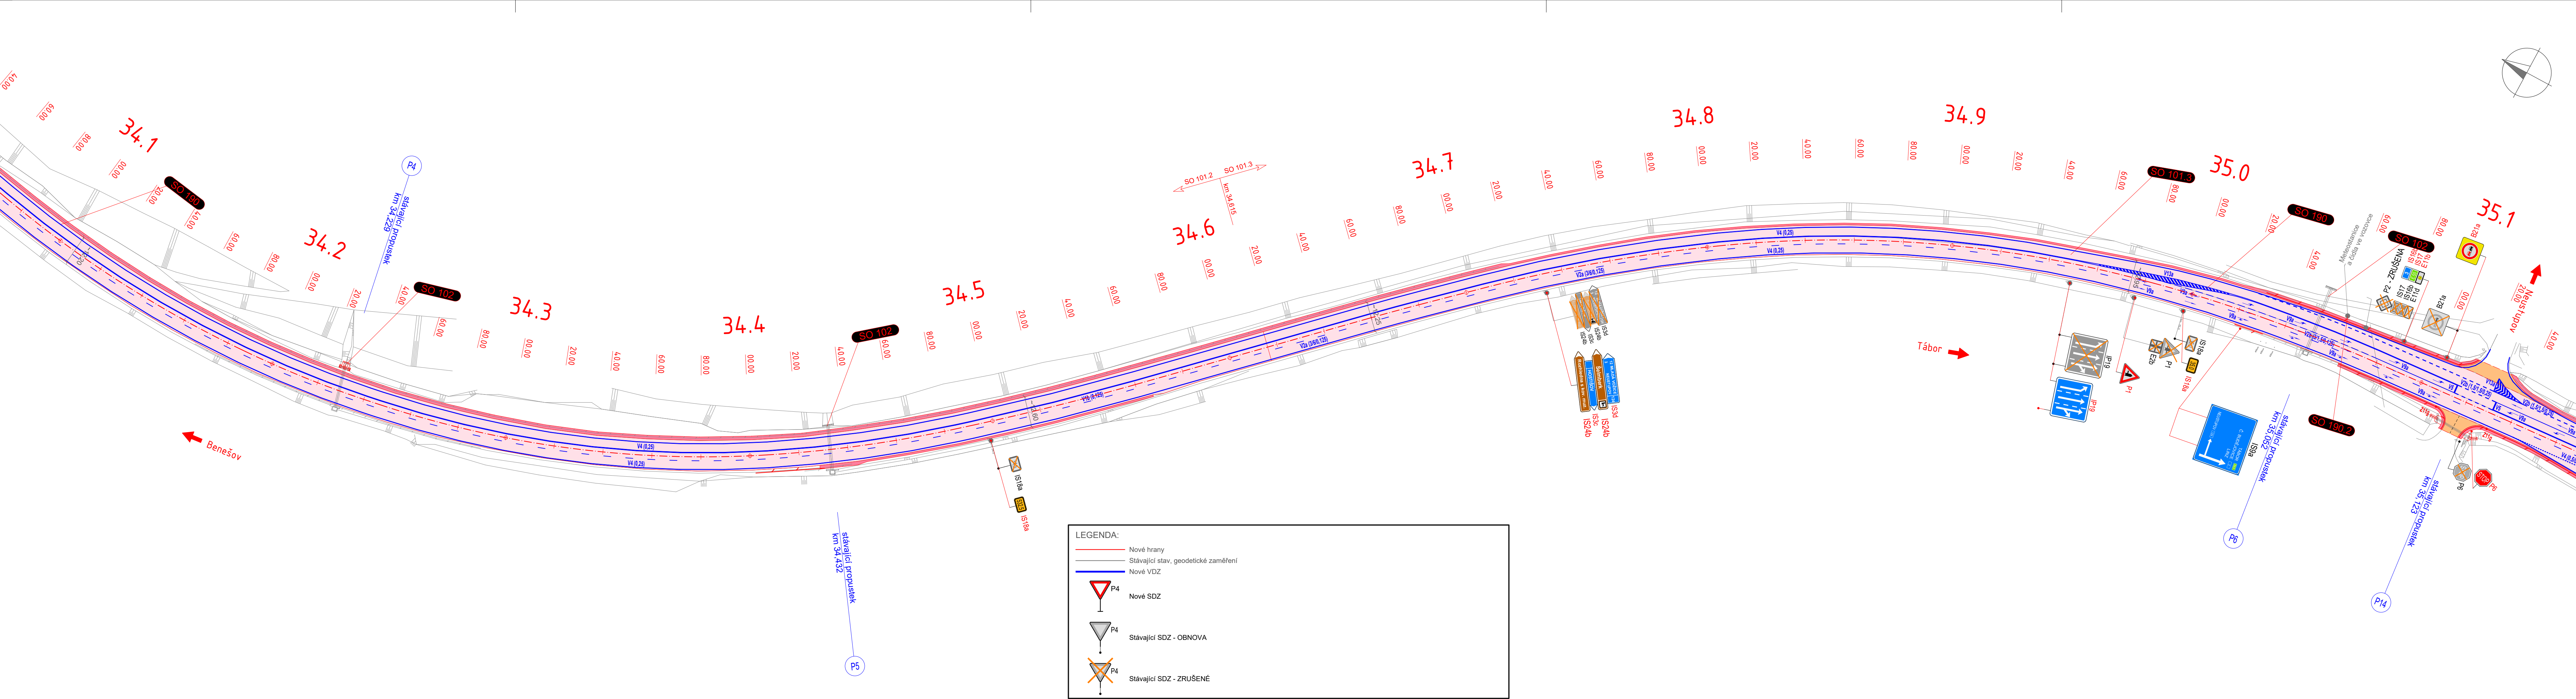

a			
b			
c			
č.	text změny - odůvodnění	datum	podpis
Název stavby:	I/3 Votice - Oldřichovec oprava povrchu a odvodnění komunikace		Číslo objektu: 190
Objednatel stavby:	 ŘEDITELSTVÍ SILNIC A DÁLNIC s. p. Čerčanská 2023/12, 140 00 Praha 4 - Krč		Razítko: Kontroloval: Datum: Podpis:
Zhotovitel stavby:	 M - SILNICE a.s. Husova 1697, Bílé Předměstí, 530 03 Pardubice		Razítko: Kontroloval: Datum: Podpis:
Koordinátor RDS:	 M - PROJEKCE s.r.o. Resslova 956/13, 500 02 Hradec Králové		Razítko: Kontroloval: Datum: Podpis:

ČISTOPIS

Souřadnicový systém S-JTSK, Výškový systém Bp			
Návrh/vypracoval:	Zodpovědný projektant:	Generální ředitel:	Zhotovitel:
Karel Láška	Karel Láška	ING. PETR HÁJEK	
Podpis:	Podpis:	Ředitel atelieru Liberec:	
Technická kontrola:	Hlavní inženýr projektu:		
DAVID SENOHRÁBEK, DI.S	Karel Láška		
Podpis:	Podpis:	ING. JIŘÍ EHRENBARGER	
Kraj: STŘEDOČESKÝ KRAJ		Čís. zakázky:	26-024-02
Katastr. úz.: Votice, Hostišov, Kouty u Smilkova		Čís. akce:	-
Objednatel: M - SILNICE a.s., Husova 1697, Bílé Předměstí, 530 03 Pardubice		Datum:	04/2026
Objekt: SO 190		Formát:	6x A4
Svislé s vodorovné dopravní značení v km 31,450 - 37,357		Měřítko:	1:1000
Příloha: Situace dopravního značení Č.3		Stupeň:	RDS
		Čís. přílohy:	2.3