


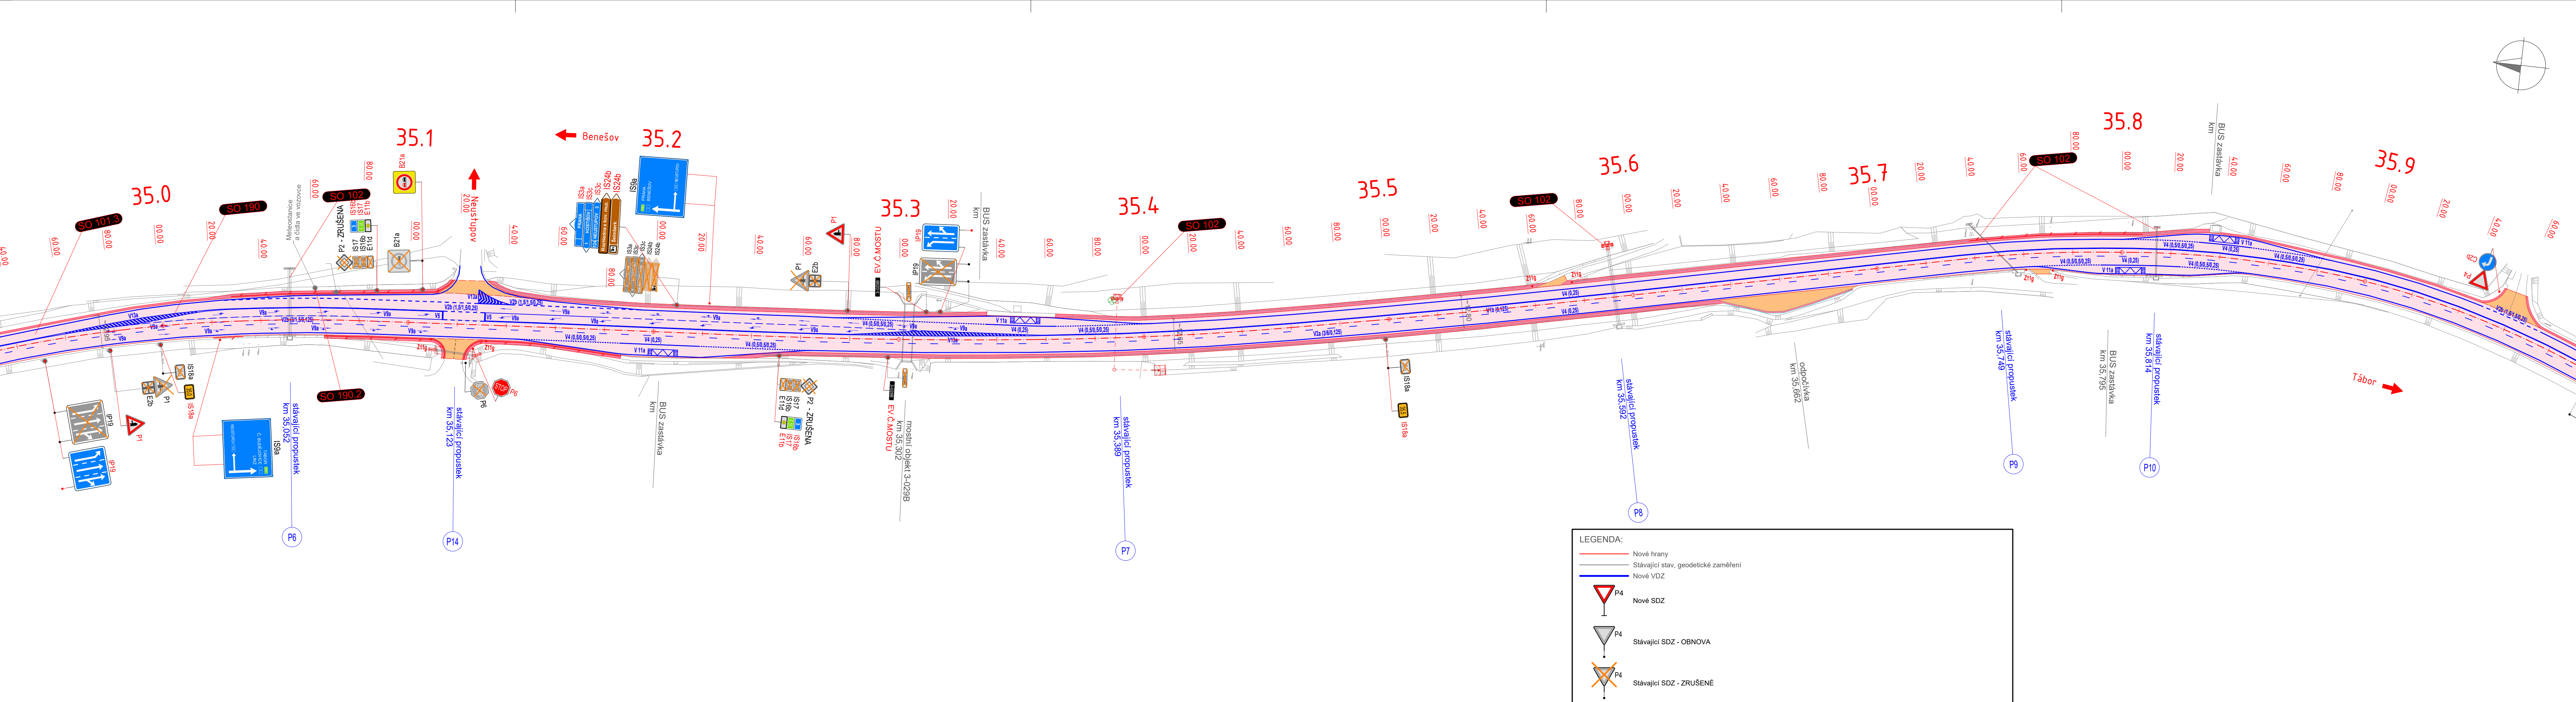

a			
b			
c			
č.	text změny - odůvodnění	datum	podpis
Název stavby: I/3 Votice - Oldřichovec oprava povrchu a odvodnění komunikace		Číslo objektu: 190	
Objednatel stavby: ŘEDITELSTVÍ SILNIC A DÁLNIC Čerčanská 2023/12, 140 00 Praha 4 - Krč		Razítko: Kontroloval: Datum: Podpis:	
Zhotovitel stavby: M-SILNICE M - SILNICE a.s. Husova 1697, Bílé Předměstí, 530 03 Pardubice		Razítko: Kontroloval: Datum: Podpis:	
Koordinační RDS: M - PROJEKCE Resslova 956/13, 500 02 Hradec Králové		Razítko: Kontroloval: Datum: Podpis:	

ČISTOPIS

Souřadnicový systém S-JTSK, Výškový systém Bpv			
Návrh/vypracoval: Karel Láska Podpis: <i>Karel Láska</i>	Zodpovědný projektant: Karel Láska Podpis: <i>Karel Láska</i>	Generální ředitel: ING. PETR HÁJEK Ředitel ateliéru Liberec: ING. JIŘÍ EHRENBARGER	Zhotovitel: M - PROJEKCE s.r.o. Resslova 956/13, 500 02 Hradec Králové
Technická kontrola: DAVID SENOHRÁBEK, DiS Podpis: <i>David Senohrábek</i>	Hlavní inženýr projektu: Karel Láska Podpis: <i>Karel Láska</i>		
Kraj: STŘEDOČESKÝ KRAJ Katastr. úz.: Votice, Hostišov, Kouty u Smilkova Objednatel: M - SILNICE a.s., Husova 1697, Bílé Předměstí, 530 03 Pardubice		Čís. zakázky: 26-024-02 Čís. akce: - Datum: 04/2026 Formát: 6x A4 Měřítko: 1:1000 Stupeň: RDS Čís. přílohy: 2.4	
Objekt: SO 190 Svislé s vodorovné dopravní značení v km 31,450 - 37,357			
Příloha: Situace dopravního značení Č.4			