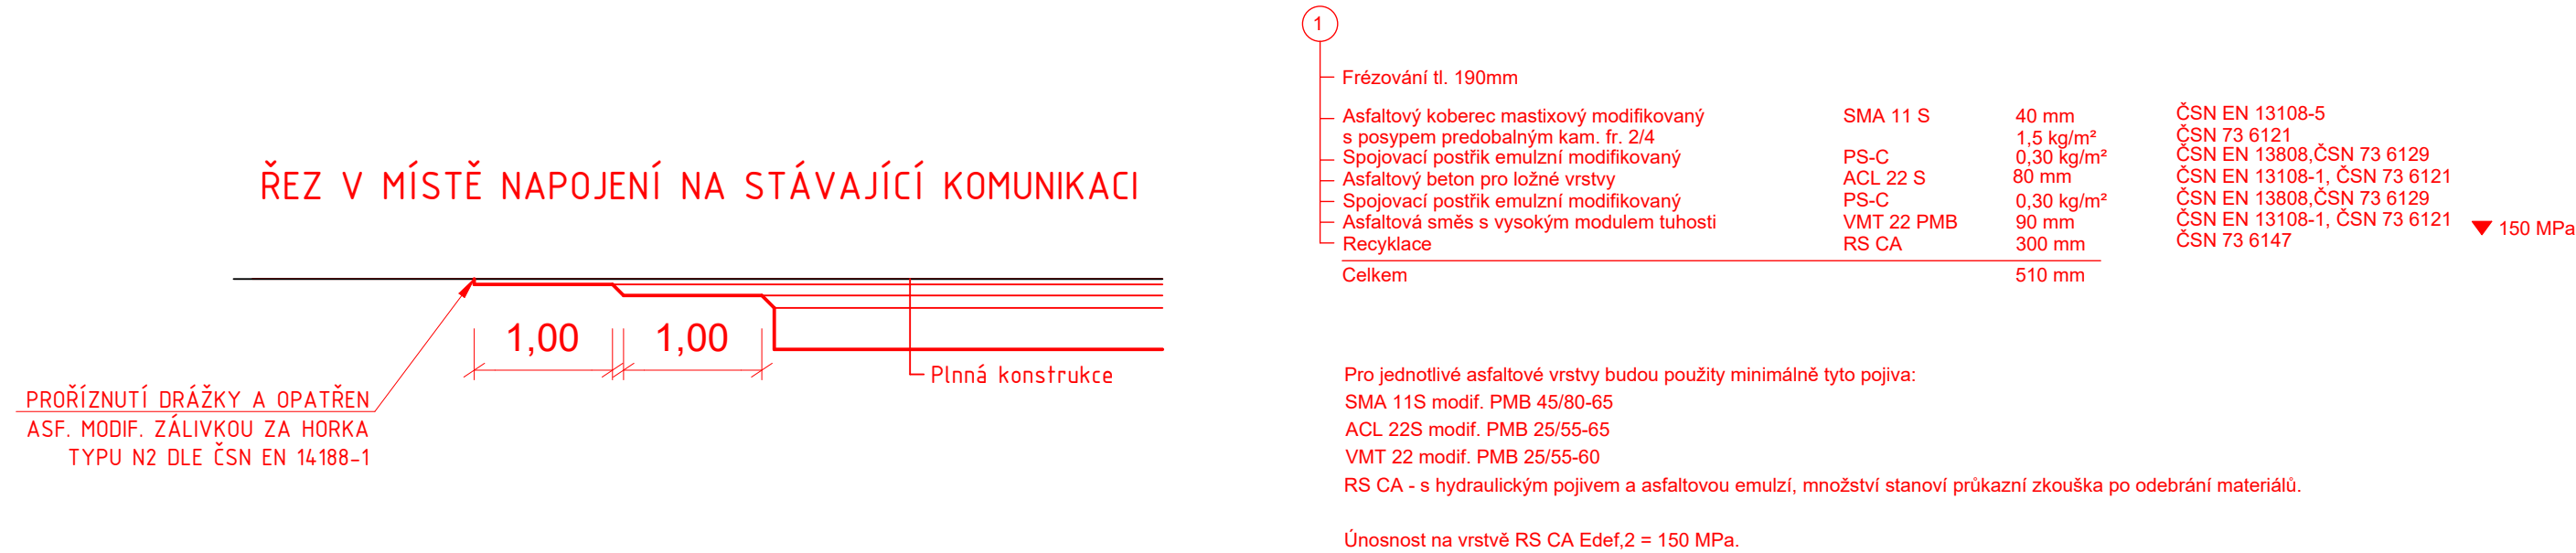
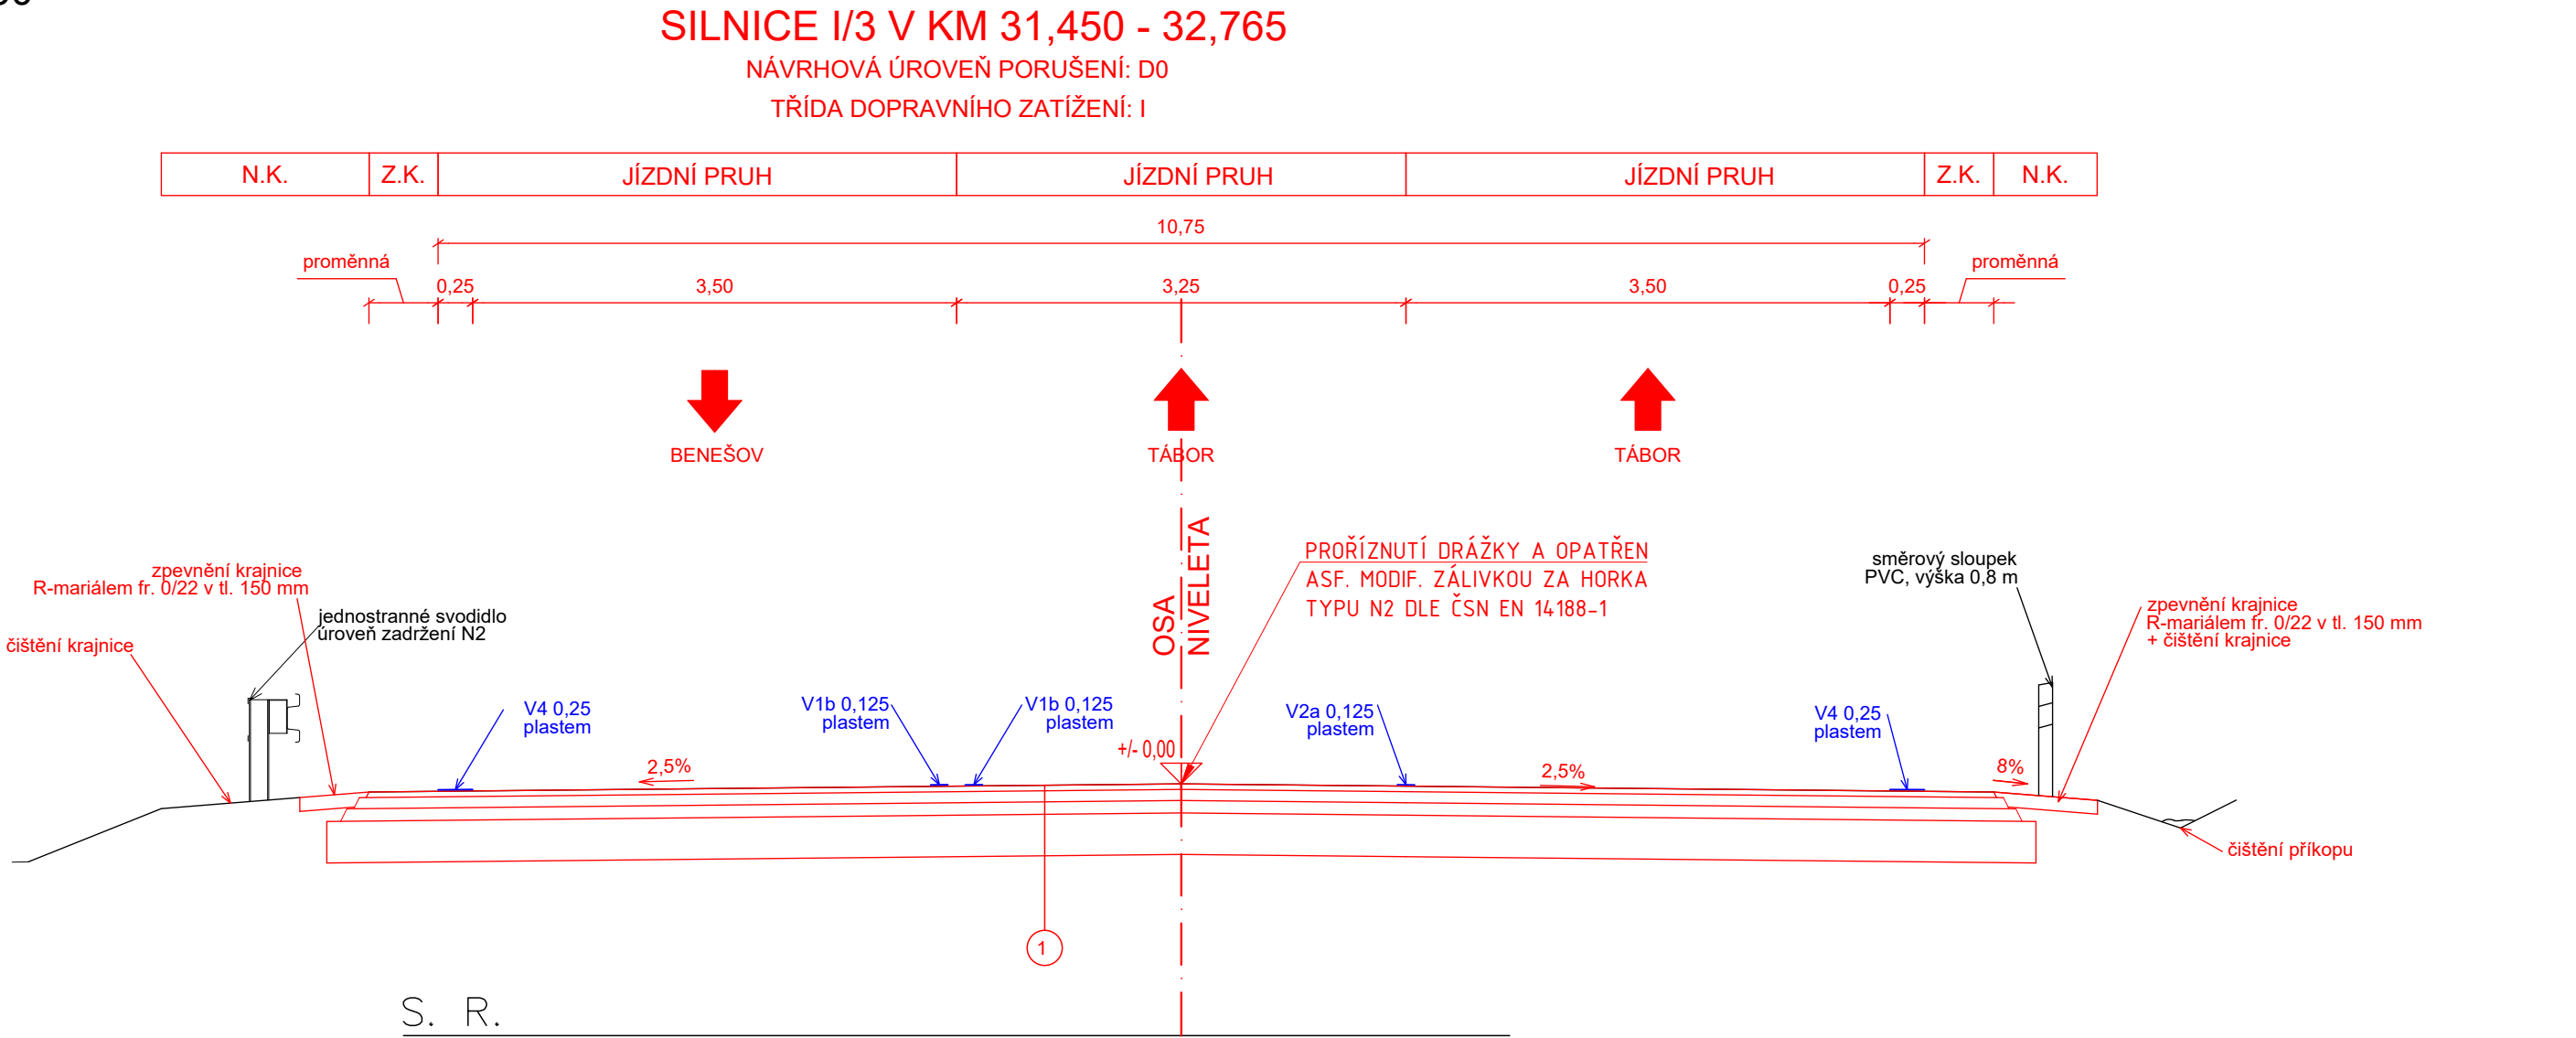


VZOROVÉ PŘÍČNÉ ŘEZY
M 1:50



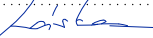
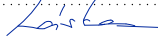
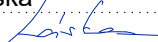
1	Frézování tl. 190mm			
	Asfaltový koberec mastixový modifikovaný s posypem predobalným kam, fr. 2/4	SMA 11 S	40 mm	ČSN EN 13108-5
	Spojovací postřik emulzní modifikovaný	PS-C	1,5 kg/m ²	ČSN 73 6121
	Asfaltový beton pro ložné vrstvy	ACL 22 S	0,30 kg/m ²	ČSN EN 13808, ČSN 73 6129
	Spojovací postřik emulzní modifikovaný	PS-C	80 mm	ČSN EN 13108-1, ČSN 73 6121
	Asfaltová směs s vysokým modulem tuhosti	PS-C	0,30 kg/m ²	ČSN EN 13808, ČSN 73 6129
	Recyklace	RS CA	90 mm	ČSN EN 13108-1, ČSN 73 6121
	Celkem		300 mm	ČSN 73 6147
			510 mm	▼ 150 MPa

Pro jednotlivé asfaltové vrstvy budou použity minimálně tyto pojiva:
SMA 11S modif. PMB 45/80-65
ACL 22S modif. PMB 25/55-65
VMT 22 modif. PMB 25/55-60
RS CA - s hydraulickým pojivem a asfaltovou emulzí, množství stanoví průkazná zkouška po odebrání materiálů.

Únosnost na vrstvě RS CA Edef,2 = 150 MPa.

a			
b			
c			
č.	text změny - odůvodnění	datum	podpis
Název stavby:	I/3 Votice - Oldřichovec oprava povrchu a odvodnění komunikace		Číslo objektu: 101.1
Objednatel stavby:	 ŘEDITELSTVÍ SILNIC A DÁLNIC s. p. Čerčanská 2023/12, 140 00 Praha 4 - Krč		Razítko: Kontroloval: Datum: Podpis:
Zhotovitel stavby:	 M - SILNICE a.s. Husova 1697, Bílé Předměstí, 530 03 Pardubice		Razítko: Kontroloval: Datum: Podpis:
Koordinátor RDS:	 M - PROJEKCE s.r.o. Resslova 956/13, 500 02 Hradec Králové		Razítko: Kontroloval: Datum: Podpis:

ČISTOPIS

Souřadnicový systém S-JTSK, Výškový systém Bpv			
Navrhl/vypracoval: Karel Láska Podpis: 	Zodpovědný projektant: Karel Láska Podpis: 	Generální ředitel: ING. PETR HÁJEK Ředitel ateliéru Liberec: ING. JIŘÍ EHRENBERGER	Zhotovitel:  M - PROJEKCE M - PROJEKCE s.r.o. Resslova 956/13, 500 02 Hradec Králové
Technická kontrola: DAVID SENOHRÁBEK, DiS Podpis: 	Hlavní inženýr projektu: Karel Láska Podpis: 		

Kraj: STŘEDOČESKÝ KRAJ	Čís. zakázky:	26-024-02
Katastr. úz.: Votice	Čís. akce:	-
Objednatel: M - SILNICE a.s., Husova 1697, Bílé Předměstí, 530 03 Pardubice	Datum:	04/2026
Objekt: SO 101.1 Oprava silnice I/3 v km 31,450 - 32,765	Formát:	3x A4
	Měřítko:	1:50
	Stupeň:	RDS
	Čís. přílohy:	
Příloha: Vzorové příčné řezy	4.	Souprava: