



M 1:50


SILNICE I/3 V KM 35.100

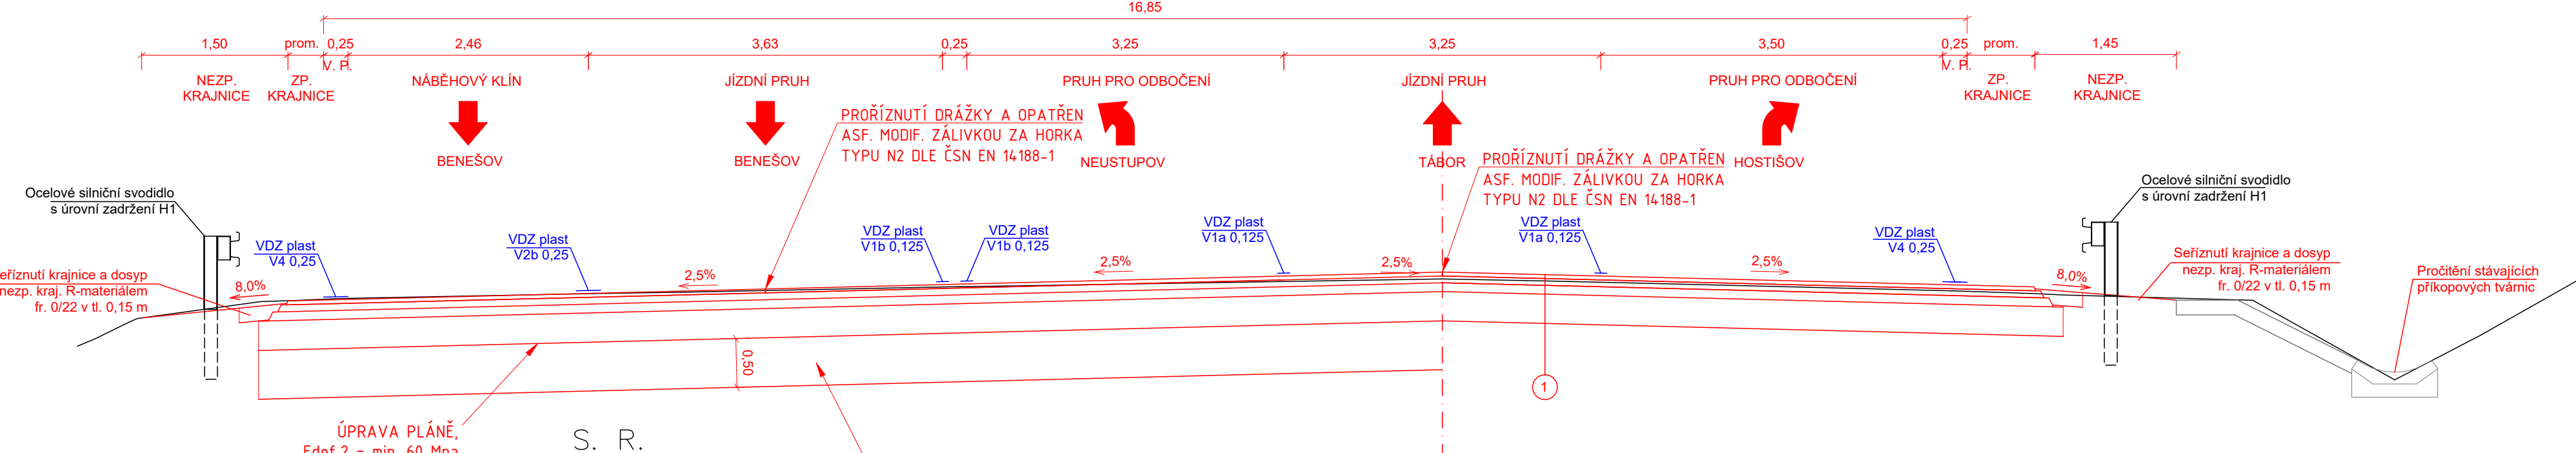

VÁŽÍCÍ MÍSTO NA SILNICI I/3 V KM 36.400

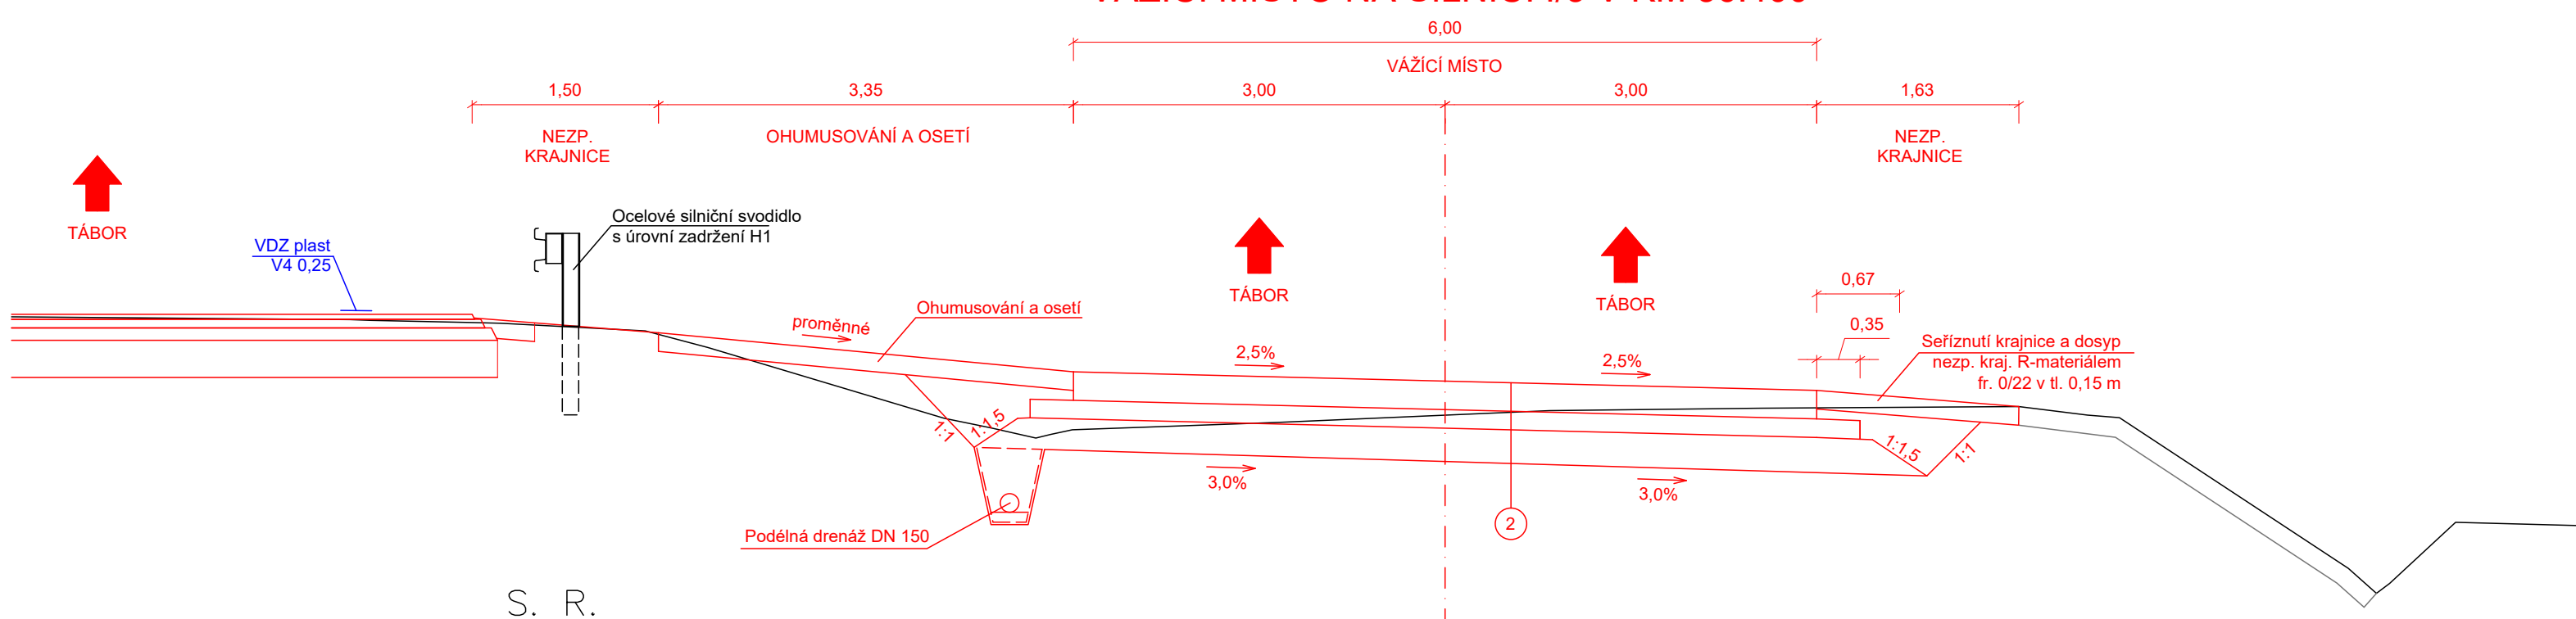

PROŘÍZNUTÍ DRÁŽKY A OPATŘENÍ
ASF. MODIF. ZÁLIVKOU ZA HORKA
TYPU N2 DLE ČSN EN 14188-1

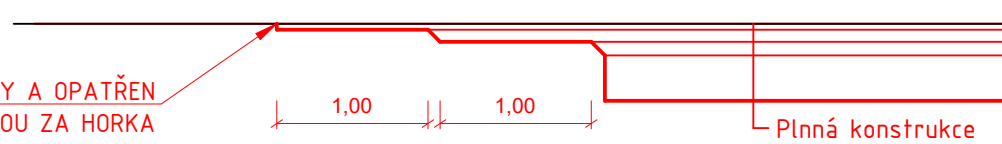

1	Frézování tl. 210mm			
	Asfaltový koberec mastixový modifikovaný s přesypem pískobáhem kam. fr. 2/4	SMA 11 S	40 mm	ČSN EN 13108-5
	Spojovací postřik emulzní modifikovaný	PS-C	1,5 kg/m ²	ČSN 73 6121
	Asfaltový beton pro ložné vrstvy modifikovaný	ACCL 22 S	0,30 kg/m ²	ČSN EN 13808, ČSN 73 6129
	Spojovací postřik emulzní modifikovaný	PS-C	80 mm	ČSN EN 13108-1, ČSN 73 6121
	Asfaltová směs s vysokým modulem tuhosti	VTM 22 PMB	0,30 kg/m ²	ČSN EN 13808, ČSN 73 6129
	Recyklace	RST CA	90 mm	ČSN EN 13108-1, ČSN 73 6121
			300 mm	ČSN 73 6147
	Celkem		510 mm	▼ 150 MF

2	Frézování a vybourání stávající konstrukce		
	Cementobetonový kryt pro obrusné vrstvy	CB I	230 mm ČSN EN 13 877-1, ČSN 73 6123-1
	Geotextilie (o plošné hmotnosti)		500g/m ²
	Vrstva ze směsi stmelené cementem	SC C ₁₀	150 mm ČSN EN 14227-1, ČSN 73 6126-1
	Štěrkodrt	ŠDa	250 mm ČSN EN 13285

Celkem	630 mm		
Asfaltové rozjezdy/ napojení na stávající komunikace			
Frézování tl. 120mm			
Asfaltový beton pro obrusné vrstvy modifikovaný	ACO 11+	40 mm	ČSN EN 13108-1, ČSN 73 6121
Spojovací postřik emulzní modifikovaný	P-S-C	0,30 kg/m ²	ČSN EN 13808, ČSN 73 6129
Asfaltový beton pro ložní vrstvy modifikovaný	ACL 22 S	80 mm	ČSN EN 13108-1, ČSN 73 6121
Spojovací postřik emulzní modifikovaný	P-S-C	0,30 kg/m ²	ČSN EN 13808, ČSN 73 6129

POZNÁMKA:
U cementobetonového krytu
bude těsnění spár provedeno asfaltovou zálivkou,
nebo pomocí těsnícího profilu.

Pro jednotlivé asfaltové vrstvy budou použity minimálně tyto pojiva:

SMA 11S modif. PMB 45/80-65
ACL 22S modif. PMB 25/55-65
VMT 22 modif. PMB 25/55-60
RS CA + s hydraulickým pojivem a asfaltovou emulzí, množství stanoví průkazní zkouška po odebrání materiálů.
ACO 11+ modif. PMB 45/80-65

Únosnost na vrstvě RS CA Edef.2 = 150 MPa.

a			
b			
c			
č.	text změny - odůvodnění	datum	podpis
Název stavby: I/3 Votice - Oldřichovec oprava povrchu a odvodnění komunikace		Číslo objektu: 101.2 101.3	
Objednatel stavby:  ŘEDITELSTVÍ SILNIC A DÁLNIC ŘEDITELSTVÍ SILNIC A DÁLNIC s. p. Čerčanská 2023/12, 140 00 Praha 4 - Krč		Razítko: Kontroloval: Datum: Podpis:	
Zhotovitel stavby:  M - SILNICE M - SILNICE a.s. Husova 1697, Bílé Předměstí, 530 03 Pardubice		Razítko: M - SILNICE a.s. Pardubice, Husova 1697 IČO 421 95 888 Obchodní závod ÚH .5 Trabantská 290/31, 190 15 Praha 9 Kontroloval: Datum: Podpis:	
Koordinátor RDS:  M - PROJEKCE M - PROJEKCE s.r.o. Ressova 956/13, 500 02 Hradec Králové		Razítko: Kontroloval: Datum: Podpis:	

ČISTOPIS

Navrh/Vypracoval: Karel Láška		Zodpovědný projektant: Karel Láška		Souřadnicový systém S-JTSK, Výškový systém Bpv	
Podpis:		Podpis:		Zhotovitel:	
Technická kontrola: DAVID SENOHRÁBEK, DIS		Hlavní inženýr projektu: Karel Láška		 M - PROJEKCE	
Podpis:		Podpis:		M - PROJEKCE s.r.o. Resslova 956/13, 500 02 Hradec Králové	
		ING. PETR HÁJEK Ředitel atelieru Liberec:			
		ING. JIŘÍ EHRENBERGER			

Kraj: STŘEDOČESKÝ KRAJ		Čís. zakázky: 26-024-02	
Katastr. úz.: Votice, Hostišov, Kouty u Smilkova		Čís. akce:	
Objednatel: M - SILNICE a.s., Husova 1697, Bílé Předměstí, 530 03 Pardubice		Datum: 04/2026	
Objekt:		Formát: 6x A4	
SO 101.2 - Oprava silnice I/3 v km 32,765 - 34,615		Měřítko: 1:50	
SO 101.3 - Oprava silnice I/3 v km 34,615 - 37,357		Stupeň:	
		RDS	
Příloha:		Čís. přílohy:	
Vzorové příčné řezy SO 101.3		4.4	