


M 1:50

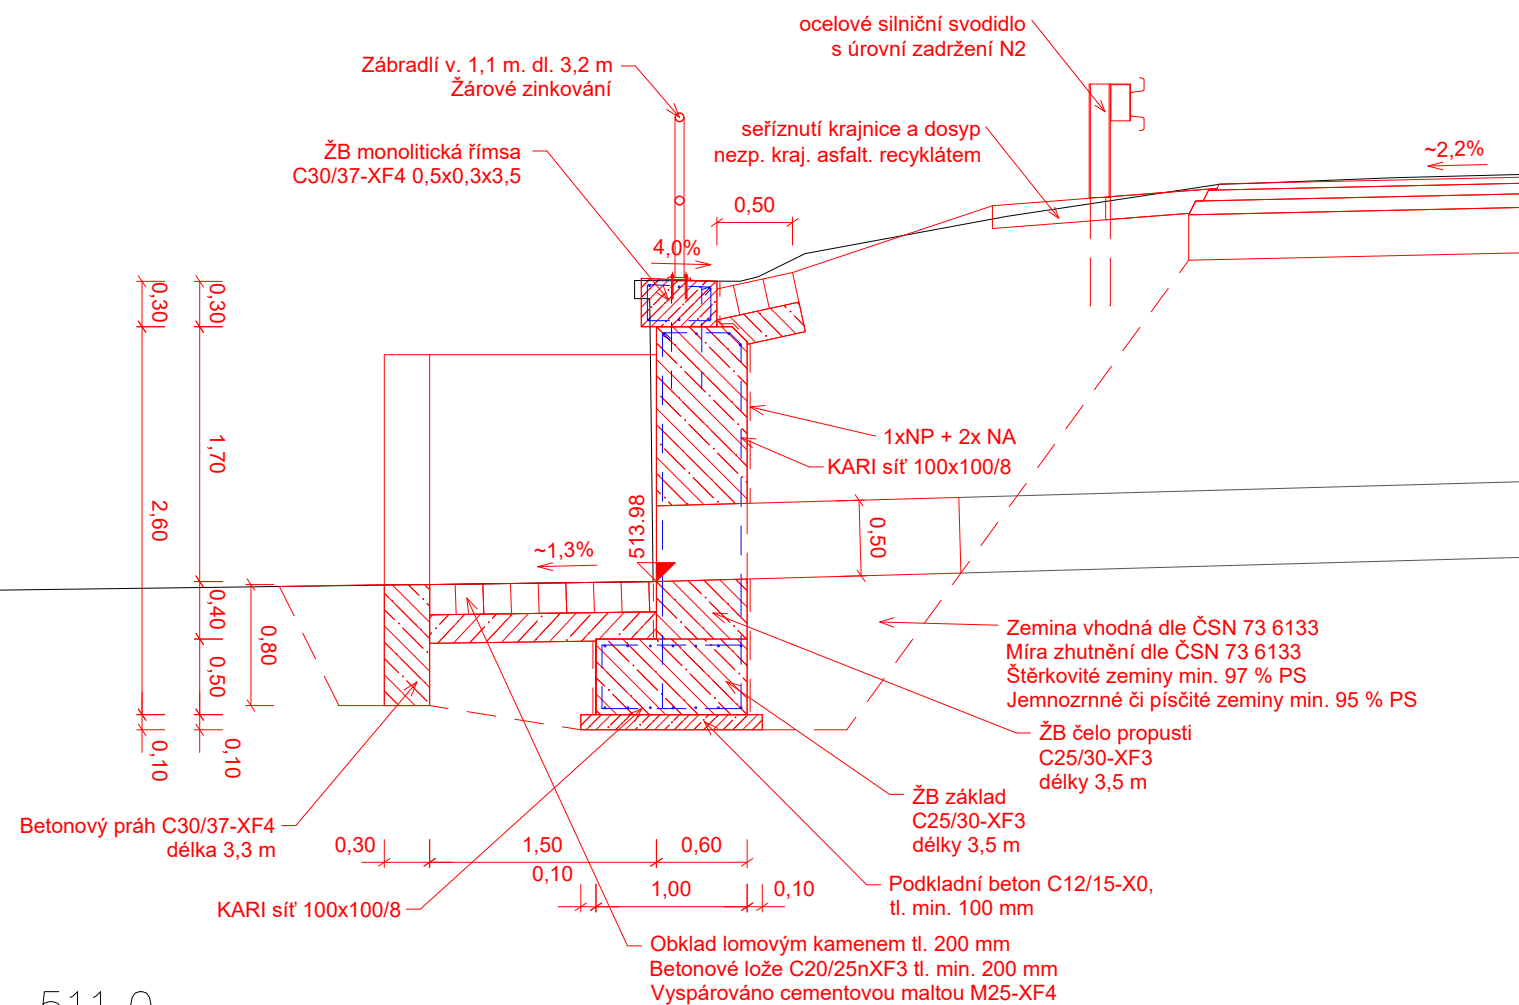

POZNÁMKA:
Čelo a základ propustku jsou vyztuženy KARI sítí 100x100/8 při povrchu.
Římsa je vyztužena viz vzor vyztužení římsy za technickou zprávou.
Mezi KARI sítěmi v základu bude umístěn distanční kozlík z betonářské
vyztuže v rozteči 900 - 1200 mm.

a			
b			
c			
č.	text změny - odůvodnění	datum	podpis

Název stavby: I/3 Votice - Oldřichovec oprava povrchu a odvodnění komunikace	Číslo objektu: 102
---	------------------------------

Objednatel stavby:  ŘEDITELSTVÍ SILNIC A DÁLNIC ŘEDITELSTVÍ SILNIC A DÁLNIC s. p. Čerčanská 2023/12, 140 00 Praha 4 - Krč	<i>Razítko:</i> <i>Kontroloval:</i> <i>Datum:</i> <i>Podpis:</i>
--	--

Zhotovitel stavby:  M - SILNICE a.s. Husova 1697, Bílé Předměstí, 530 03 Pardubice	Razítko: M - SILNICE a.s. Pardubice, Husova 1697 IČO 421 96 868 oblastní závod UH a.s. 24 Trabantská 290/31, 190 15 Praha 9 Kontroloval: Datum: Podpis:
---	--

Koordinátor RDS:  M - PROJEKCE M - PROJEKCE s.r.o. Resslova 956/13, 500 02 Hradec Králové	<i>Razítko:</i> <i>Kontroloval:</i> <i>Datum:</i> <i>Podpis:</i>
---	--

ČISTOPIS

Souřadnicový systém S-JTSK, Výškový systém Bpv			
Navrhl/vypracoval: Karel Láska Podpis: 	Zodpovědný projektant: Karel Láska Podpis: 	Generální ředitel: ING. PETR HÁJEK	Zhotovitel:  M - PROJEKCE
Technická kontrola: DAVID SENOHRÁBEK, DiS Podpis: 	Hlavní inženýr projektu: Karel Láska Podpis: 	Ředitel ateliéru Liberec: ING. JIŘÍ EHRENBARGER	M - PROJEKCE s.r.o. Resslova 956/13, 500 02 Hradec Králové

Kraj: STŘEDOČESKÝ KRAJ	Čís. zakázky:	26-024-02
Katastr. úz.: Votice, Hostišov, Kouty u Smilkova	Čís. akce:	-
Objednatel: M - SILNICE a.s., Husova 1697, Bílé Předměstí, 530 03 Pardubice	Datum:	04/2026
Objekt: SO 102 Oprava propustků	Formát:	2x A4
	Měřítko:	1:50
	Stupeň:	Souprava:
	RDS	
Příloha: Propustek v km 33,342	Čís. přílohy:	2.1