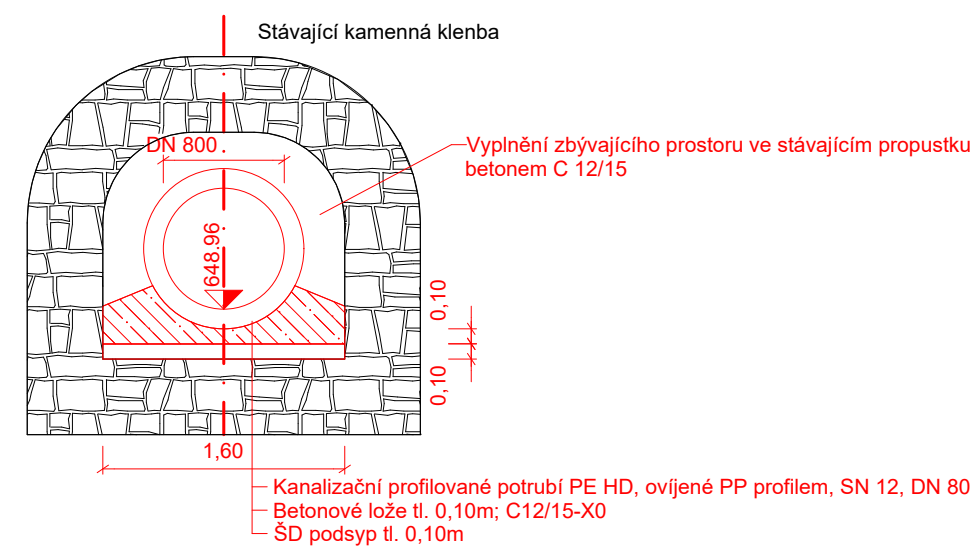


|   | Y             | X            | Z      |
|---|---------------|--------------|--------|
| 1 | -1098340.5576 | -733026.7104 | 469,45 |
| 2 | -1098349.6336 | -733003.3825 | 648.25 |

**POZNÁMKA:**  
Jímka propustku je vyztužena KARI sítí 100x100/8 při povrchu.  
Mezi KARI sítěmi v základu bude umístěn distanční kozlík z betonářské  
výztuže v rozteči 900 - 1200 mm.

|   |                         |   |        |
|---|-------------------------|---|--------|
| a   |                         |   |        |
| b   |                         |   |        |
| c   |                         |   |        |
| č.   | text změny - odůvodnění | datum   | podpis |
| Název stavby: <b>I/3 Votice - Oldřichovce oprava povrchu a odvodnění komunikace</b>   |                         | Číslo objektu: <b>102</b>   |        |
| Objednatel stavby:<br><br><b>ŘEDITELSTVÍ SILNIC A DÁLNIC</b><br><br><b>ŘEDITELSTVÍ SILNIC A DÁLNIC s. p.</b><br>Čerčanská 2023/12, 140 00 Praha 4 - Krč |                         | Razítko:<br><br><br>Kontroloval:<br>Datum: Podpis:                                                                                          |        |
| Zhotovitel stavby:<br><br><b>M-SILNICE</b><br><br><b>M - SILNICE a.s.</b><br>Husova 1697, Bílé Město, 530 03 Pardubice                                  |                         | Razítko:<br><br><b>M - SILNICE a.s.</b><br>Pardubice, Husova 1697<br>IČO 421 96 868<br>tiskárna závazná<br>Trabantská 280/1, 190 15 Praha 9 |        |
| Koordínátor RDS:<br><br><b>M - PROJEKCE</b><br><br><b>M - PROJEKCE s.r.o.</b><br>Reslova 956/13, 500 02 Hradec Králové                                |                         | Razítko:<br><br><br>Kontroloval:<br>Datum: Podpis:                                                                                          |        |

# ČISTOPIS

|   |  |                                                                       |  |   |  |   |  |
|---|--|-----------------------------------------------------------------------|--|---|--|---|--|
| Navrh/vypracoval:<br>Karel Láska<br>Podpis: <i>[Signature]</i>   |  | Zodpovědný projektant:<br>Karel Láska<br>Podpis: <i>[Signature]</i>   |  | Generální ředitel:<br>ING. PETR HÁJEK<br>Ředitel atelieru Liberec:<br>ING. JIŘÍ EHRENBERGER             |  | Soudradnicový systém S-JTSK, Výškový systém Bpv<br>Zhotovitel:<br><br>M - PROJEKCE s.r.o.<br>Reslavoja 956/13, 500 02 Hradec Králové |  |
| Technická kontrola:<br>DAVID SENOHRÁBEK, DIS<br>Podpis: <i>[Signature]</i>                                                                                           |  | Hlavní inženýr projektu:<br>Karel Láska<br>Podpis: <i>[Signature]</i> |  |   |  |   |  |
| Kraj: STŘEDOČESKÝ KRAJ<br>Katastr. úz.: Votice, Hostišov, Kouty u Smilkova<br>Objednatel: M - SILNICE a.s., Husova 1697, Bílé Předměstí, 530 03 Pardubice<br>Objekt: |  |                                                                       |  | Čís. zakázky: 26-024-02<br>Čís. akce: -<br>Datum: 04/2026<br>Formát: 10x A4<br>Měřítko: 1:50<br>Stupeň: |  | Souprava:   |  |
| SO 102<br>Oprava propustků   |  |                                                                       |  | RDS   |  |   |  |
| Příloha:   |  |                                                                       |  | Čís. přílohy:                                                                                           |  | 2.7   |  |
| Propustek v km 36,589   |  |                                                                       |  |   |  |   |  |