

BENEŠOV

TÁBOR

SKLONOVÉ POMĚRY:

MĚŘÍTKA:
1: 1000, 1: 100.

KÓTY NIVELETY:


KÓTY TERÉNU:

SROVNÁVACÍ ROVINA:

STANICENÍ:

VZDÁLENOST PŘÍŘEZŮ:

SMĚROVÉ POMĚRY:



a				
b				
c				
č	text změny - odůvodnění		datum	podpis
Název stavby: I/3 Votice - Oldřichovec oprava povrchu a odvodnění komunikace		Číslo objektu: 101.2 101.3		
Objednatel stavby: ŘEDITELSTVÍ SILNIC A DÁLNIC		Razisko:		
ŘEDITELSTVÍ SILNIC A DÁLNIC s. p. Čertánská 2023/12, 140 00 Praha 4 - Krč		Kontroloval: Datum: Podpis:		
Zhotovitel stavby: M-SILNICE		Razisko:		
M - SILNICE a.s. Pardubice, Husova 1697 ICO 421 86 868 IČO 421 86 868 Tratimská 2002/1, 190 15 Praha 9		Kontroloval: Datum: Podpis:		
Koordínátor RDS: M - PROJEKCE		Razisko:		
M - PROJEKCE s.r.o. Resslova 956/13, 500 02 Hradec Králové		Kontroloval: Datum: Podpis:		

Hlavní vypracoval: Karel Láska		Zodpovědný projektant: Karel Láska		Generální reditel: ING. PETR HÁJEK		Souřadnicový systém S-JTSK, Výškový systém Bpv	
Podpis: Karel Láska		Podpis: Karel Láska		Reditel ateliéru Liberec: ING. JIŘÍ EHRENBARGER		Zhotovitel: M - PROJEKCE	
Technická kontrola: DAVID SENOHRÁBEK, DIS		Hlavní inženýr projektu: Karel Láska		Podpis: Karel Láska		M - PROJEKCE s.r.o. Resslova 956/13, 500 02 Hradec Králové	
Podpis: Karel Láska		Podpis: Karel Láska		Podpis: Karel Láska		RDS	
Kraj: STŘEDOČESKÝ KRAJ		Katastr. úz.: Votice, Hostšův, Kouty u Smilkova		Objednatel: M - SILNICE a.s., Husova 1697, Bílé Předměstí, 530 03 Pardubice		Čís. zakázky: 26-024-02	
Objekt: SO 101.2 - Oprava silnice I/3 v km 32,765 - 34,615		SO 101.3 - Oprava silnice I/3 v km 34,615 - 37,357		Datum: 04/2026		Formát: 18x A4	
Priloha: Podélný profil č.2		Čís. přílohy: 3.2		Stupeň: 1:1000/100		Souprava: 18x A4	