


SITUACE STAVBY SO 101.3
M 1:1000

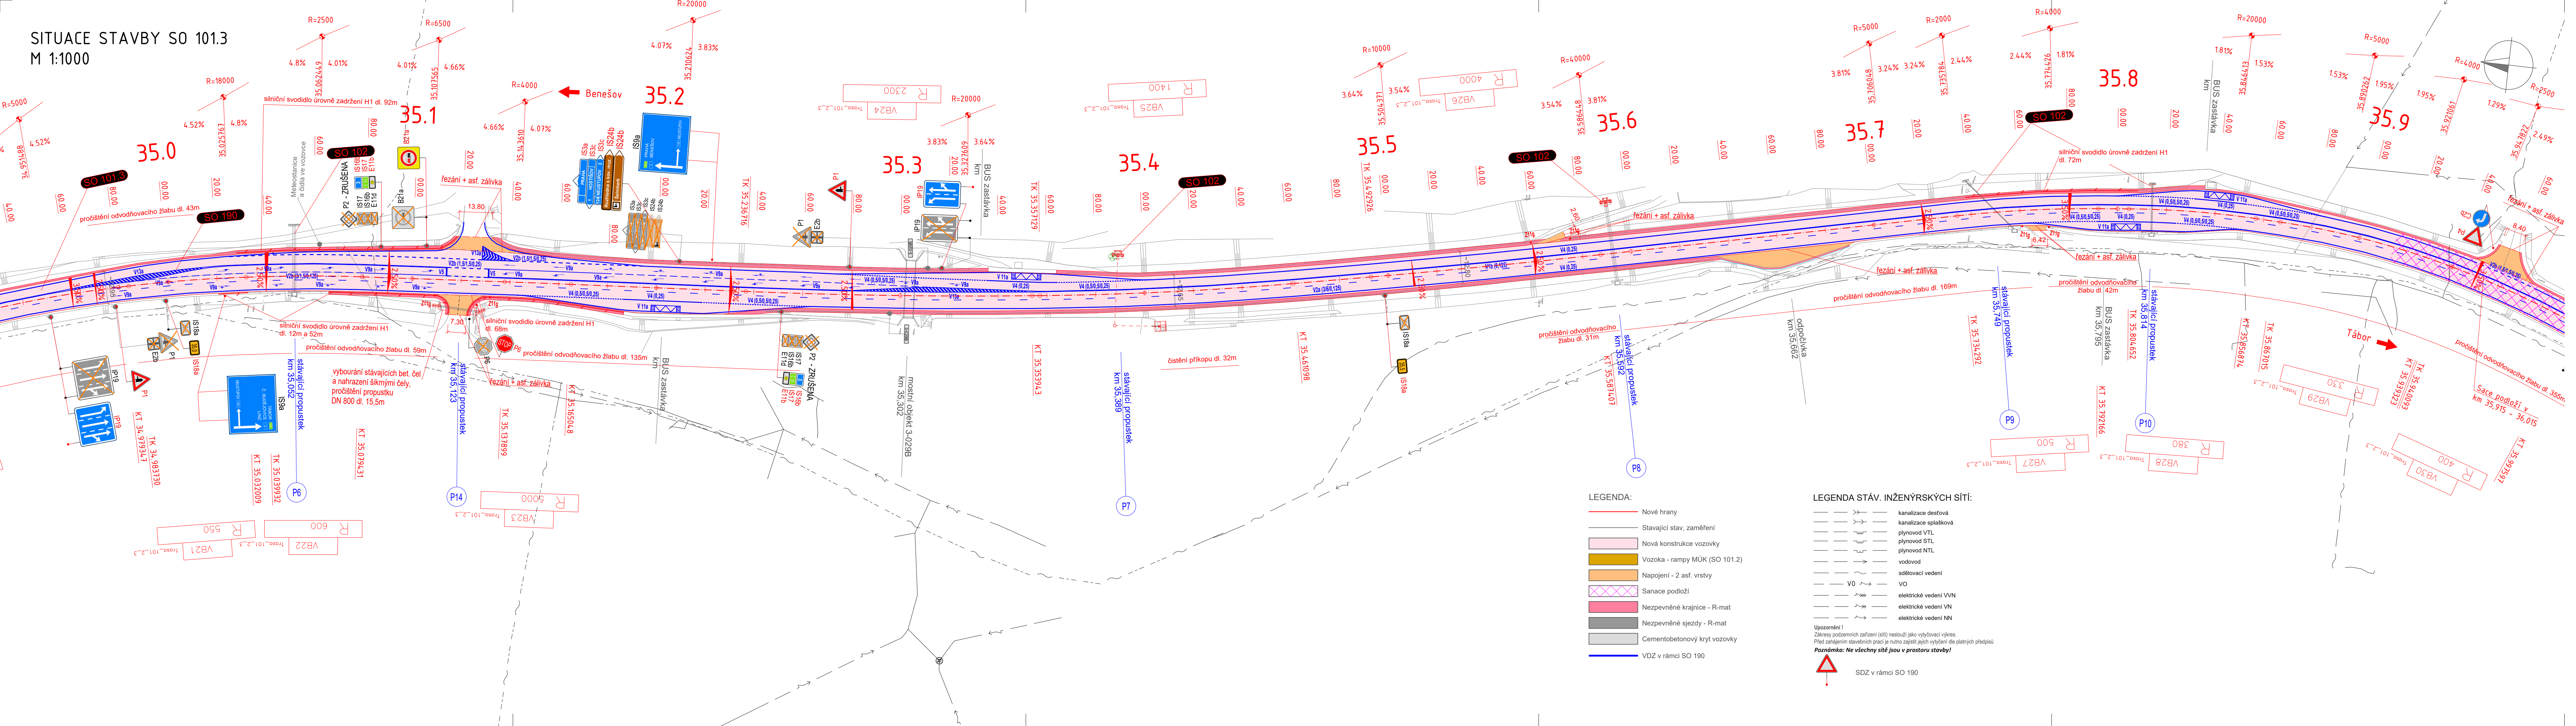

- LEGENDA:
- Nové hrany
 - Stávající stav, zaměření
 - Nová konstrukce vozovky
 - Vozoka - rampy MUK (SO 101.2)
 - Napojení - 2. asf. vrstvy
 - Sanace podloží
 - Nezpevněné krajnice - R-mat
 - Nezpevněné sjezdy - R-mat
 - Cementobetonový kryt vozovky
 - VDZ v rámci SO 190

- LEGENDA STÁV. INŽENÝRSKÝCH SÍTÍ:
- kanalizace dešťová
 - kanalizace splašková
 - plynovod VTL
 - plynovod STL
 - plynovod NTL
 - vodovod
 - sálavací vedení
 - VO
 - elektrické vedení VVN
 - elektrické vedení VN
 - elektrické vedení NN
- Upozornění I
Zakresy podzemních zařízení (sítí) neslouží jako výřezový výkres.
Před zahájením stavebních prací je nutno zajistit jejich vyřízení dle platných předpisů.
Poznámka: Ne všechny sítě jsou v prostoru stavby!

a			
b			
c			
č.	text změny - odůvodnění	datum	podpis
Název stavby: I/3 Votice - Oldřichovec oprava povrchu a odvodnění komunikace		Číslo objektu: 101.2 101.3	
Objednatel stavby: ŘEDITELSTVÍ SILNIC A DÁLNIC s. p. Čerčanská 2023/12, 140 00 Praha 4 - Krč		Razítko:	
		Kontroloval:	
		Datum:	Podpis:
Zhotovitel stavby: M - SILNICE a.s. Pardubice, Husova 1697 IČO 421 96 868 Iubazská 280/31, 190 15 Praha 9		Razítko:	
		Kontroloval:	
		Datum:	Podpis:
Koordínátor RDS: M - PROJEKCE s.r.o. Resslova 956/13, 500 02 Hradec Králové		Razítko:	
		Kontroloval:	
		Datum:	Podpis:

ČISTOPIS

Souřadnicový systém S-JTSK, Výškový systém Bpv			Zhotovitel:
Navrhl/vypracoval: Karel Láska Podpis: <i>Karel Láska</i>	Zodpovědný projektant: Karel Láska Podpis: <i>Karel Láska</i>	Generální ředitel: ING. PETR HÁJEK Ředitel atelieru Liberec: ING. JIŘÍ EHREMBERGER	 M - PROJEKCE s.r.o. Resslova 956/13, 500 02 Hradec Králové
Technická kontrola: DAVID SENOHRÁBEK, DiS Podpis: <i>David Senohrábek</i>	Hlavní inženýr projektu: Karel Láska Podpis: <i>Karel Láska</i>		
Kraj: STŘEDOČESKÝ KRAJ			Čís. zakázky: 26-024-02
Katastr. úz.: Votice, Hostišov, Kouty u Smilkova			Čís. akce: -
Objednatel: M - SILNICE a.s., Husova 1697, Bílé Předměstí, 530 03 Pardubice			Datum: 04/2026
Objekt:			Formát: 6x A4
SO 101.2 - Oprava silnice I/3 v km 32,765 - 34,615 SO 101.3 - Oprava silnice I/3 v km 34,615 - 37,357			Měřítko: 1:1000
			Stupeň: RDS
			Souprava:
Příloha:			Čís. přílohy: 2.3
Situace č. 3			