


SITUACE STAVBY SO 101
M 1:1000



a			
b			
c			
č.	text změny - odůvodnění	datum	podpis
Název stavby: I/3 Votice - Oldřichovec oprava povrchu a odvodnění komunikace		Číslo objektu: 101.2 101.3	
Objednatel stavby:  ŘEDITELSTVÍ SILNIC A DÁLNIC ŘEDITELSTVÍ SILNIC A DÁLNIC s. p. Čerčanská 2023/12, 140 00 Praha 4 - Krč		Ražičko: Kontroloval: Datum: Podpis:	
Zhotovitel stavby:  M-SILNICE M - SILNICE a.s. Husova 1697, Bílé Předměstí, 530 03 Pardubice		Ražičko: M - SILNICE a.s. Pardubice, Husova 1697 IČO 421 96 868 Lábarská ulice ul. 5. Trabantská 2003/1, 190 15 Praha 9 Kontroloval: Datum: Podpis:	
Koordinátor RDS:  M-PROJEKCE M - PROJEKCE s.r.o. Ressova 956/13, 500 02 Hradec Králové		Ražičko: Kontroloval: Datum: Podpis:	

ČISTOPIS

Návštíř/výpracov: Karel Láška Podpis: <i>[Signature]</i>		Zodpovědný projektant: Karel Láška Podpis: <i>[Signature]</i>		Generální ředitel: ING. PETR HÁJEK Ředitel atelieru Liberoc: ING. JIŘÍ EHRENBARGER		Soutěžní systém S-JTSK, Výškový systém Bp Zhotovitel:	
Technická kontrola: DAVID SENOHŘÁBEK, DiS Podpis: <i>[Signature]</i>		Hlavní inženýr projektu: Karel Láška Podpis: <i>[Signature]</i>				M - PROJEKCE s.r.o. Resslova 956/13, 500 02 Hradec Králové	
Kraj: STŘEDOČESKÝ KRAJ Katastr. úz.: Volice, Hostišov, Kouty u Smolkova Objednatel: M - SILNICE a.s., Husova 1697, Bílé Předměstí, 530 03 Pardubice Objekt: SO 101.2 - Oprava silnice I/3 v km 32,765 - 34,615 SO 101.3 - Oprava silnice I/3 v km 34,615 - 37,357						Čís. zakázky: 26-024-02 Čís. akce: Datum: 04/2026 Formát: 8x A4 Měřítko: 1:1000 Stupeň:	
Příloha:						Čís. přílohy:	
Situace č. 4						2.4	