




LEGENDA:

- Nové hrany
- Stávající stav, geodetické zaměření
- Nové VDZ
- Nové SDZ
- Stávající SDZ - OBNOVA
- Stávající SDZ - ZRUŠENÉ

a			
b			
c			
č	text změny - odůvodnění	datum	podpis
Název stavby: I/3 Votice - Oldřichovec oprava povrchu a odvodnění komunikace		Číslo objektu: 190	
Objednatel stavby: ŘEDITELSTVÍ SILNIC A DÁLNIC ŘEDITELSTVÍ SILNIC A DÁLNIC s.p. Čerčanská 2023/12, 140 00 Praha 4 - Krč		Razítko: Kontroloval: Datum: Podpis:	
Zhotovitel stavby: M-SILNICE M - SILNICE a.s. Husova 1697, Bílé Předměstí, 530 03 Pardubice		Razítko: M - SILNICE a.s. Pardubice, Husova 1697 IČO 47 99 868 Tržební síť 2023/12, 140 00 Praha 4	
Koordínátor RDS: M - PROJEKCE M - PROJEKCE s.r.o. Ressova 956/13, 500 02 Hradec Králové		Razítko: M - PROJEKCE s.r.o. Ressova 956/13, 500 02 Hradec Králové	

Souřadnicový systém S-JTSK, Výškový systém Bpv			
Návrh/vypracoval: Karel Láška	Zodpovědný projektant: Karel Láška	Generální reditel: ING. PETR HÁJEK	Zhotovitel: M - PROJEKCE
Podpis: <i>Karel Láška</i>	Podpis: <i>Karel Láška</i>	Reditel ateliéru Liberec: ING. JIŘÍ EHRENBARGER	
Technická kontrola: DAVID SENOHRÁBEK, DIS	Hlavní inženýr projektu: Karel Láška		
Podpis: <i>David Senohrábek</i>	Podpis: <i>Karel Láška</i>		
Kraj: STŘEDOČESKÝ KRAJ		Čís. zakázky: 26-024-02	
Katastr. úz.: Votice, Hostišov, Kouty u Smilkova		Čís. akce: -	
Objednatel: M - SILNICE a.s., Husova 1697, Bílé Předměstí, 530 03 Pardubice		Datum: 04/2026	
Objekt: SO 190 Svislé s vodorovné dopravní značení v km 31,450 - 37,357		Formát: 8x A4	
Příloha: Situace dopravního značení Č.2		Měřítko: 1:1000	
		Stupeň: RDS	Souprava:
		Čís. přílohy: 2.2	