SITUACE STAVBY SO 101.2
M 1:1000

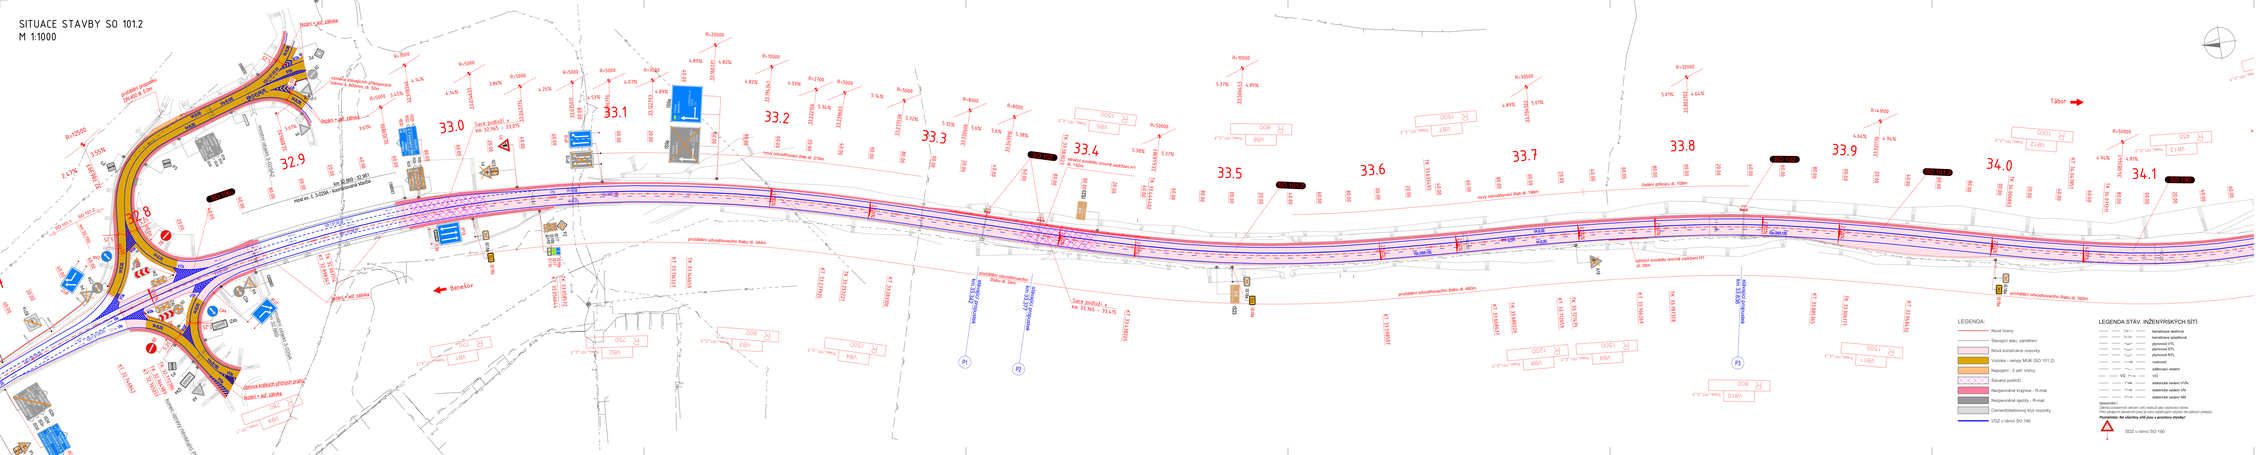

a			
b			
c			
d	text změny - odůvodnění	datum	podpis

Název stavby: I/3 Votice - Oldřichovec oprava povrchu a odvodnění komunikace	Číslo objektu: 101.2 101.3

Objednatel stavby:
ŘEDITELSTVÍ SILNIC A DÁLNIC
ŘEDITELSTVÍ SILNIC A DÁLNIC s. p.
Čerčanská 2023/12, 140 00 Praha 4 - Krč
Razítko:
Kontrolval:
Datum: Podpis:

Zhotovitel stavby:
M - SILNICE
M - SILNICE a.s.
Husova 1697, Bílé Předměstí, 530 03 Pardubice
M - SILNICE a.s.
Pardubice Nádraží 1697
Husova 1697, Bílé Předměstí
Telefonní ústředna 290201, 190 10 Praha 9
Razítko:
Kontrolval:
Datum: Podpis:

Koordinátor RDS:
M - PROJEKCE
M - PROJEKCE s.r.o.
Resslova 958/13, 500 02 Hradec Králové
Razítko:
Kontrolval:
Datum: Podpis:

KONCEPT

Souřadnicový systém S-JTSK, Výškový systém Bpv

Vypracovával: Karel Laška, Podpis:	Zodpovědný projektant: Karel Laška, Podpis:	Generální ředitel: ING. PETR HLEK, Ředitel sekce Liberec: ING. JIŘÍ DVEŘENBERGER	Zhotovitel: M - PROJEKCE s.r.o. Resslova 958/13, 500 02 Hradec Králové
Technická kontrola: DAVID SENOHRABEK, DiS Podpis:	Hlavní inženýr projektu: Karel Laška, Podpis:		

Kraj: STŘEDOČESKÝ KRAJ	Čís. zakázky: 26-024-02
Katast. úz.: Votice, Hostišov, Kloutu u Smilkova	Čís. akce:
Objednatel: M - SILNICE a.s., Husova 1697, Bílé Předměstí, 530 03 Pardubice	Datum: 03/2026
Objekt: SO 101.2 - Oprava silnice I/3 v km 32,765 - 34,615 SO 101.3 - Oprava silnice I/3 v km 34,615 - 37,357	Format: 8x A4
	Měřítko: 1:1000
	Stupeň: RDS Dopravce:
Příloha: Situace č. 1	Čís. přílohy: 2.1

Upozornění:
Zákresy podzemních inženýrských sítí nejsou ani výškově ani polohově zaměřeny a jsou pouze informativní. Je nutno dodržet ochranná pásma podzemních sítí.
Poznámka: Ne všechny uliční pisma a prvotřídní stavby!

SDZ s rámcí SO 190