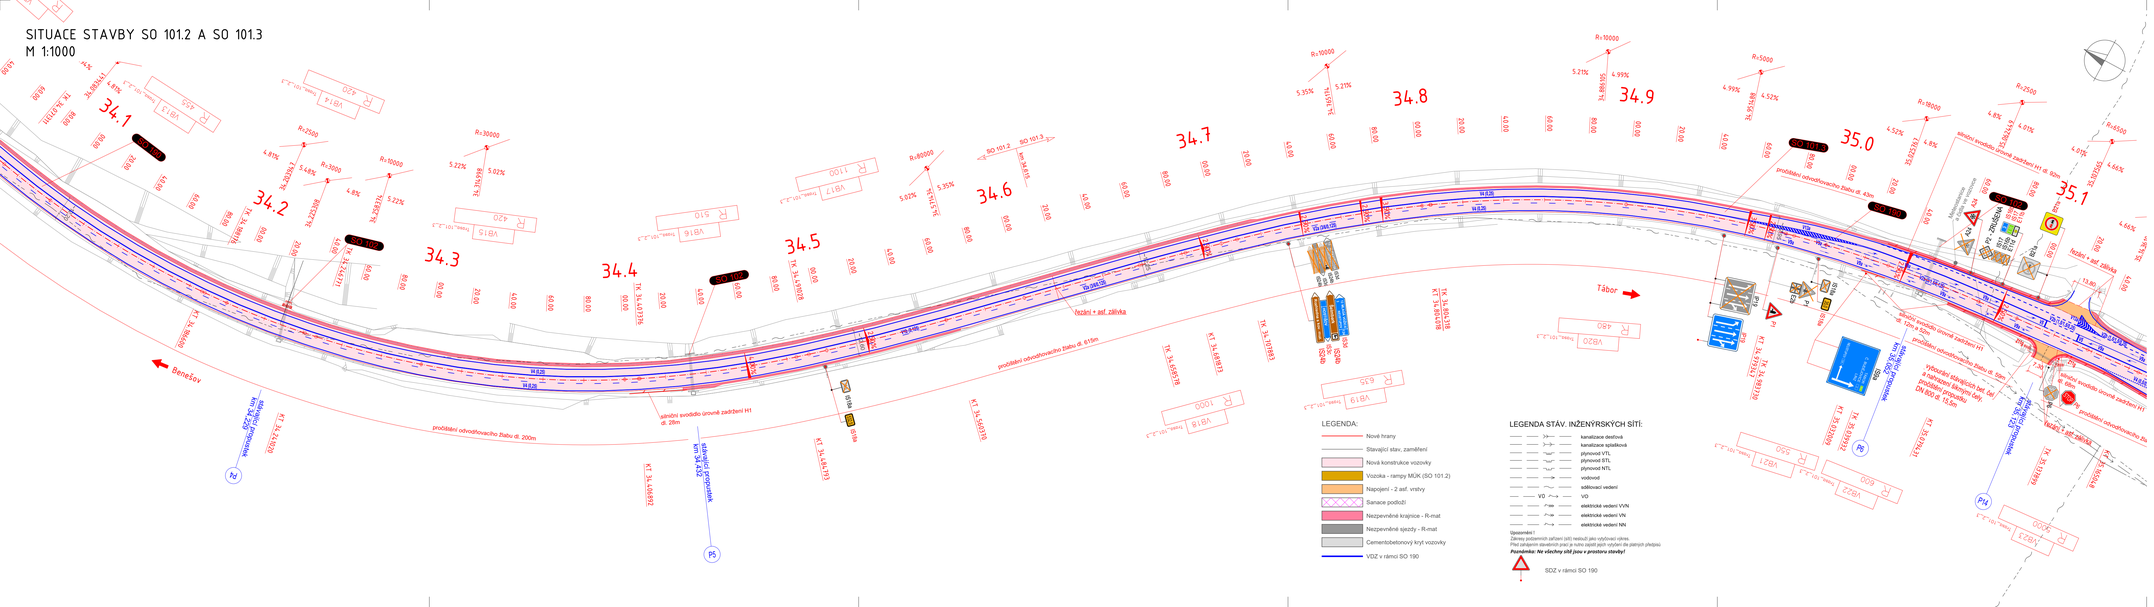SITUACE STAVBY SO 101.2 A SO 101.3
M 1:1000